

Architecture Portfolio

Presented by : Sameer Sheikh



ABOUT ME

✉ sheikhsameer.prof@gmail.com

☎ +971-522911906

📍 Dubai, United Arab Emirates

Hello, my name is Sameer Sheikh, and I am from India. I have recently relocated to Dubai and I am eager to further enhance my knowledge and skills by working with a professional firm where I can contribute effectively while continuing to learn and grow in the field of architecture.

I hold a Bachelor's degree in Architecture and completed my studies and architectural internship in India. During my internship, I gained hands-on experience in architectural drafting, design development, site coordination, and preparing detailed technical drawings. I also had the opportunity to work on drawing approval processes with major authorities such as DDA, NDMC, and DRDO, which gave me valuable exposure to regulatory compliance and project execution.

Professional Experience

Satish Kumar Mathur & Associates

Architect Trainee - Noida, Delhi NCR (2023-2024)

Tools & Skills

- AutoCAD
- SketchUp
- Revit
- Lumion
- Adobe Photoshop
- Microsoft Office
- V-Ray
- Ai Enhancement



Welcome

This portfolio presents a selection of my academic projects and professional internship work, showcasing my design approach, technical skills, and practical experience in architecture.

Together, these projects reflect my creativity, attention to detail, problem-solving abilities, and commitment to delivering functional and sustainable design solutions as I begin my professional career in architecture.



My Featured Projects

Project 01



PROPOSED RESIDENCE FOR MR. AVINASH SINGH
AT FAZIL NAGAR, KUSHINAGAR DISTRICT-27440

Project 02



PROVISION OF NEW MARRIED ACCOMMODATION
AT DEFENCE RESEARCH LABORATORY, TEZPUR

Project 03




PROPOSED DESIGN WORK FOR J&K HOUSE,
PRITHVIRAJ ROAD NEW DELHI

Project 04



PROPOSED RAJKIYA SARVODAYA. KANYA
VIDYALAYA, EAST VINOD NAGAR NEW DELHI

Project 05

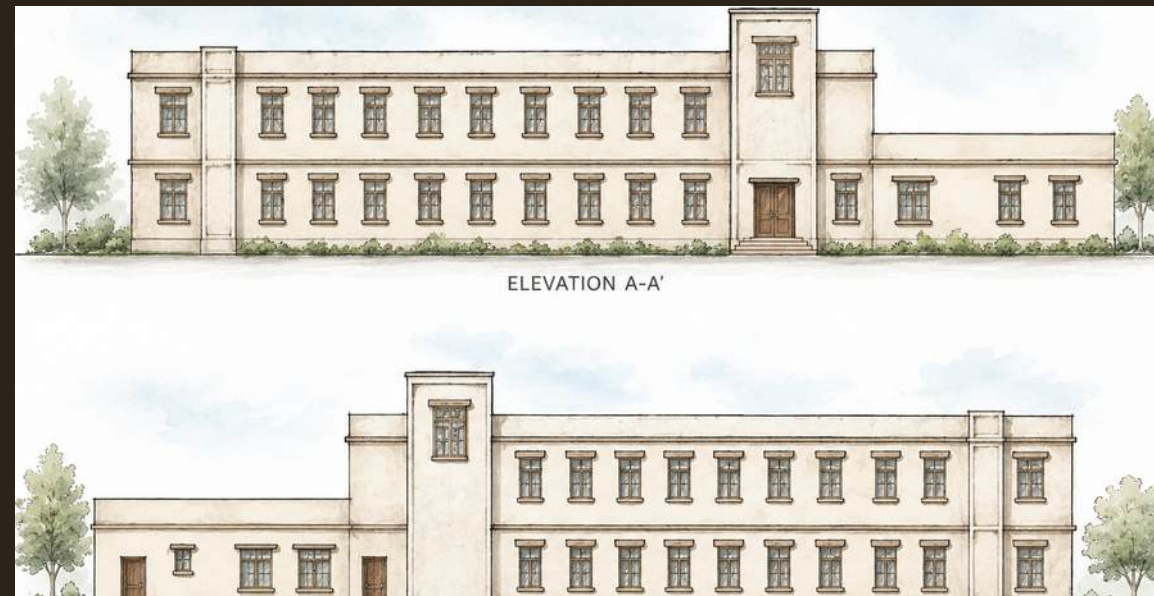

DORMATORY, BHATGAON, LUCKNOW

Project 06




MISCELLANEOUS DRAWINGS

Project 01

PROPOSED RESIDENCE FOR MR. AVINASH SINGH AT
FAZIL NAGAR, KUSHINAGAR DISTRICT-27440



PROPOSED RESIDENDCE FOR MR. AVINASH SINGH AT FAZIL NAGAR, KUSHINAGAR DISTRICT-27440

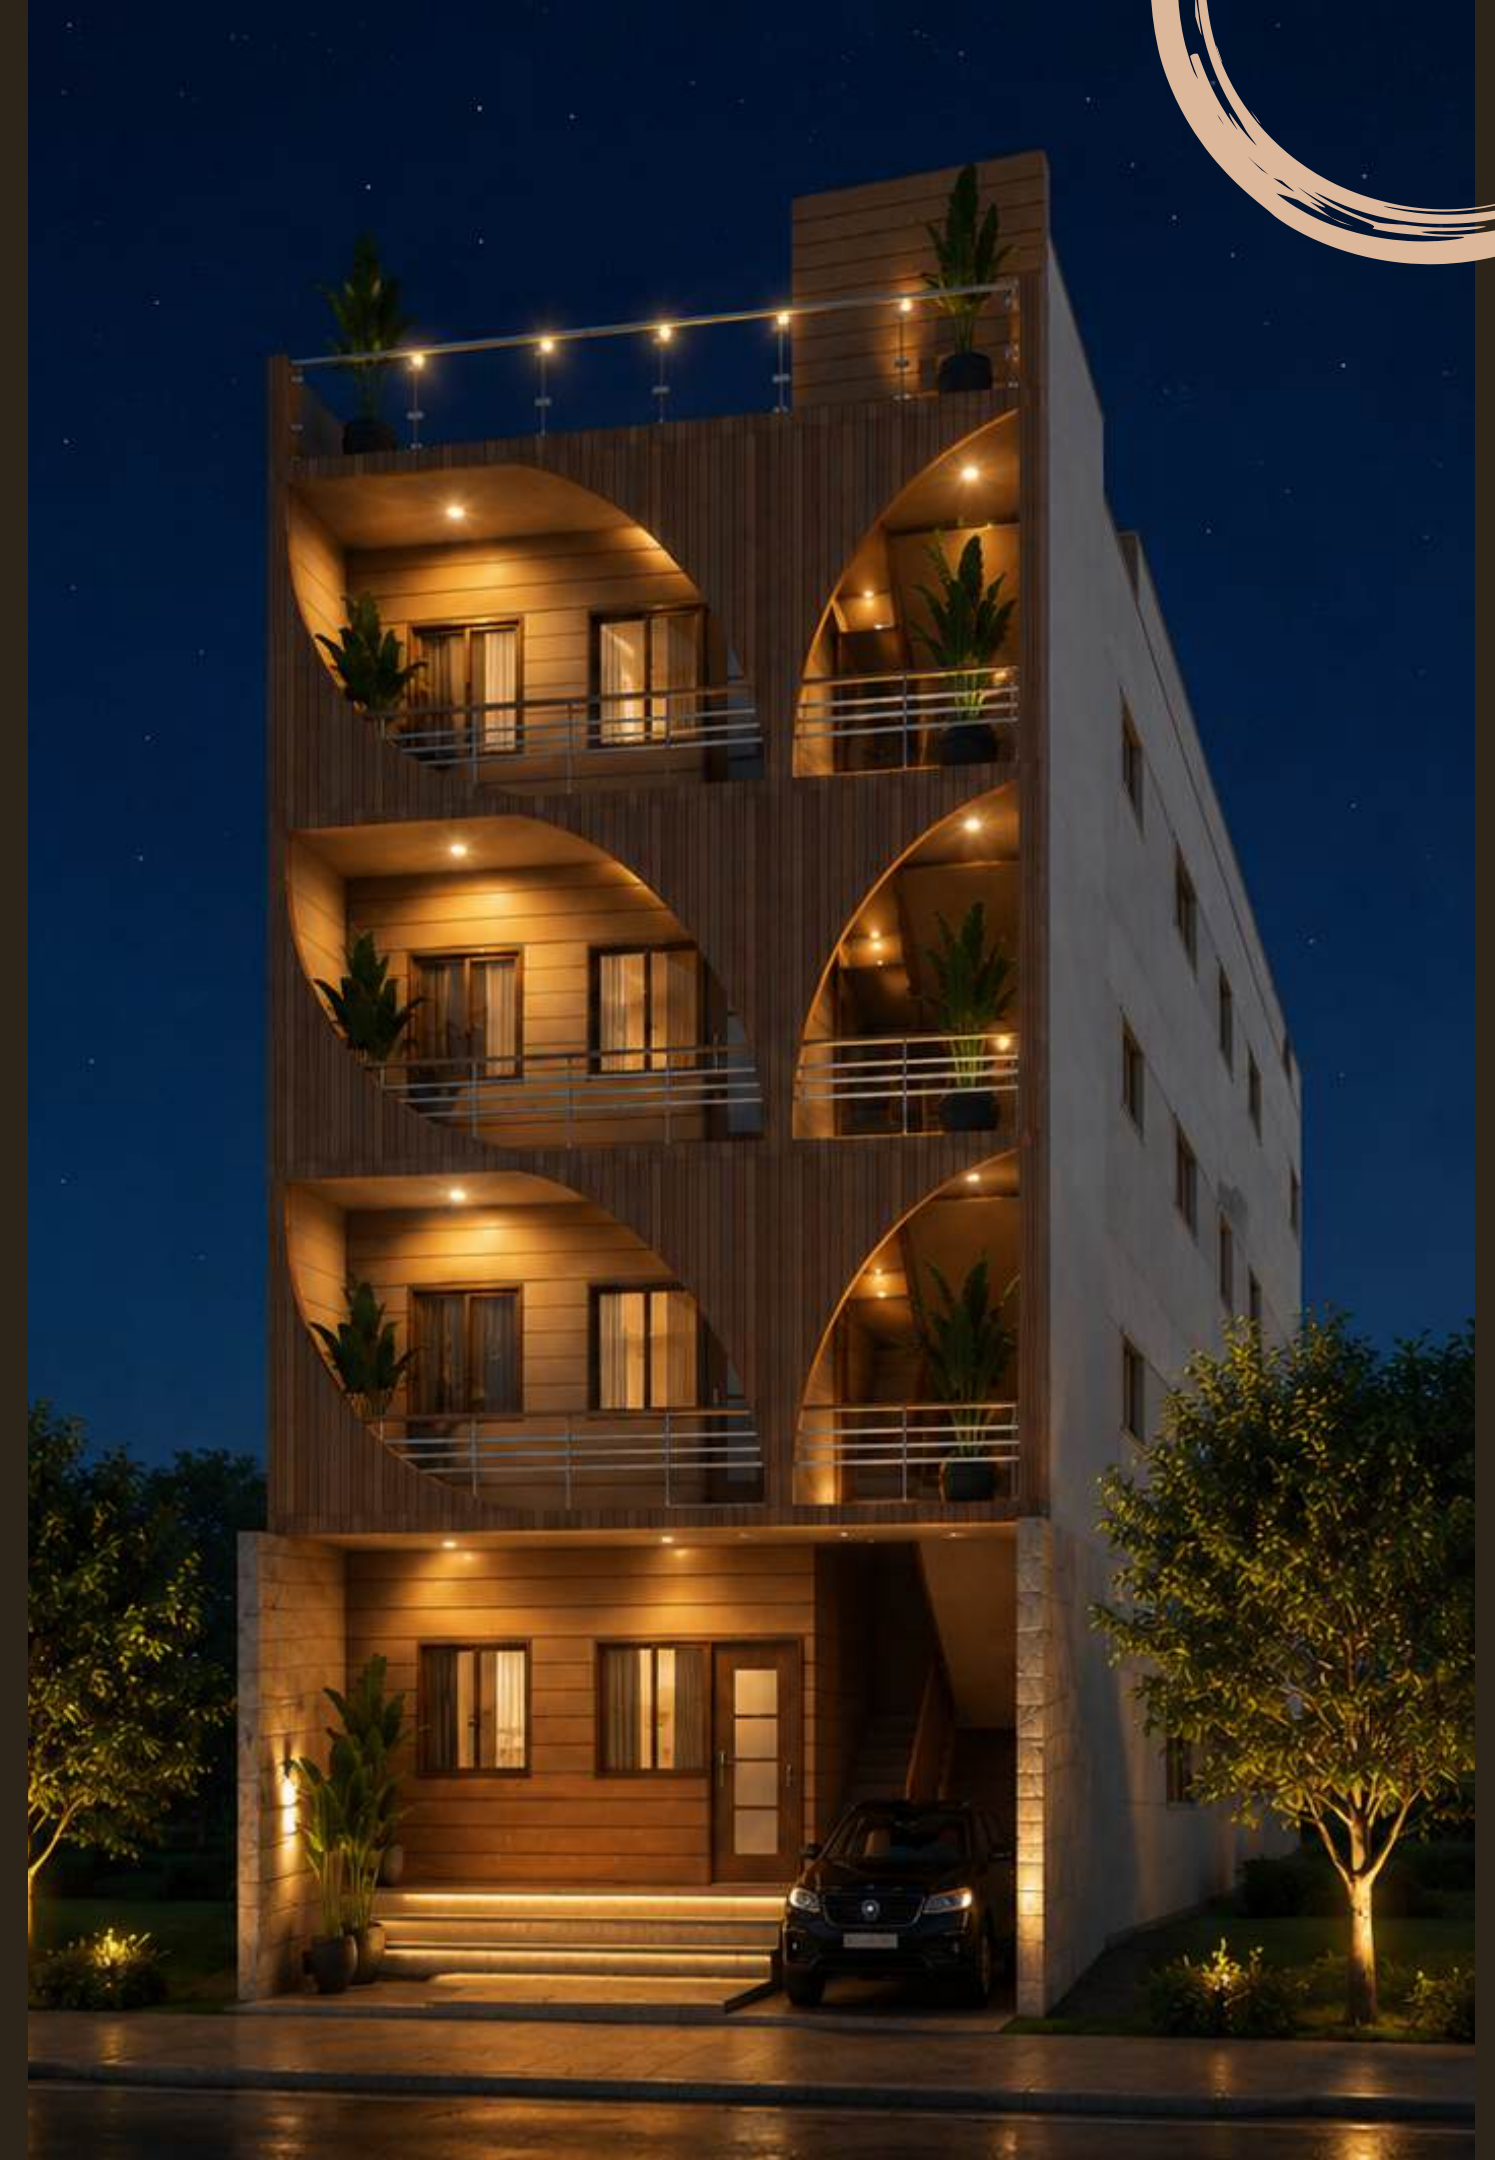

Project 02



PROPOSED DESIGN WORK FOR PROVISION OF NEW MARRIED ACCOMMODATION AT DEFENCE RESEARCH
LABORATORY (DRL), TEZPUR (ASSAM)





FIRST FLOOR PLAN

Project 03

PROPOSED DESIGN WORK FOR J&K HOUSE, PRITHVIRAJ ROAD NEW DELHI

This project involved the redesign of the reception and public interior spaces of J&K House, Prithviraj Road, New Delhi, inspired by the rich cultural heritage of Kashmir.


The design integrates traditional Kashmiri craftsmanship through intricate wood carvings, floral patterns, warm natural materials, and elegant detailing while maintaining a functional and contemporary interior.



Cultural Heritage of J&K



The objective was to create a welcoming environment that reflects the architectural identity, culture, and timeless aesthetics of Jammu & Kashmir in a modern institutional setting.

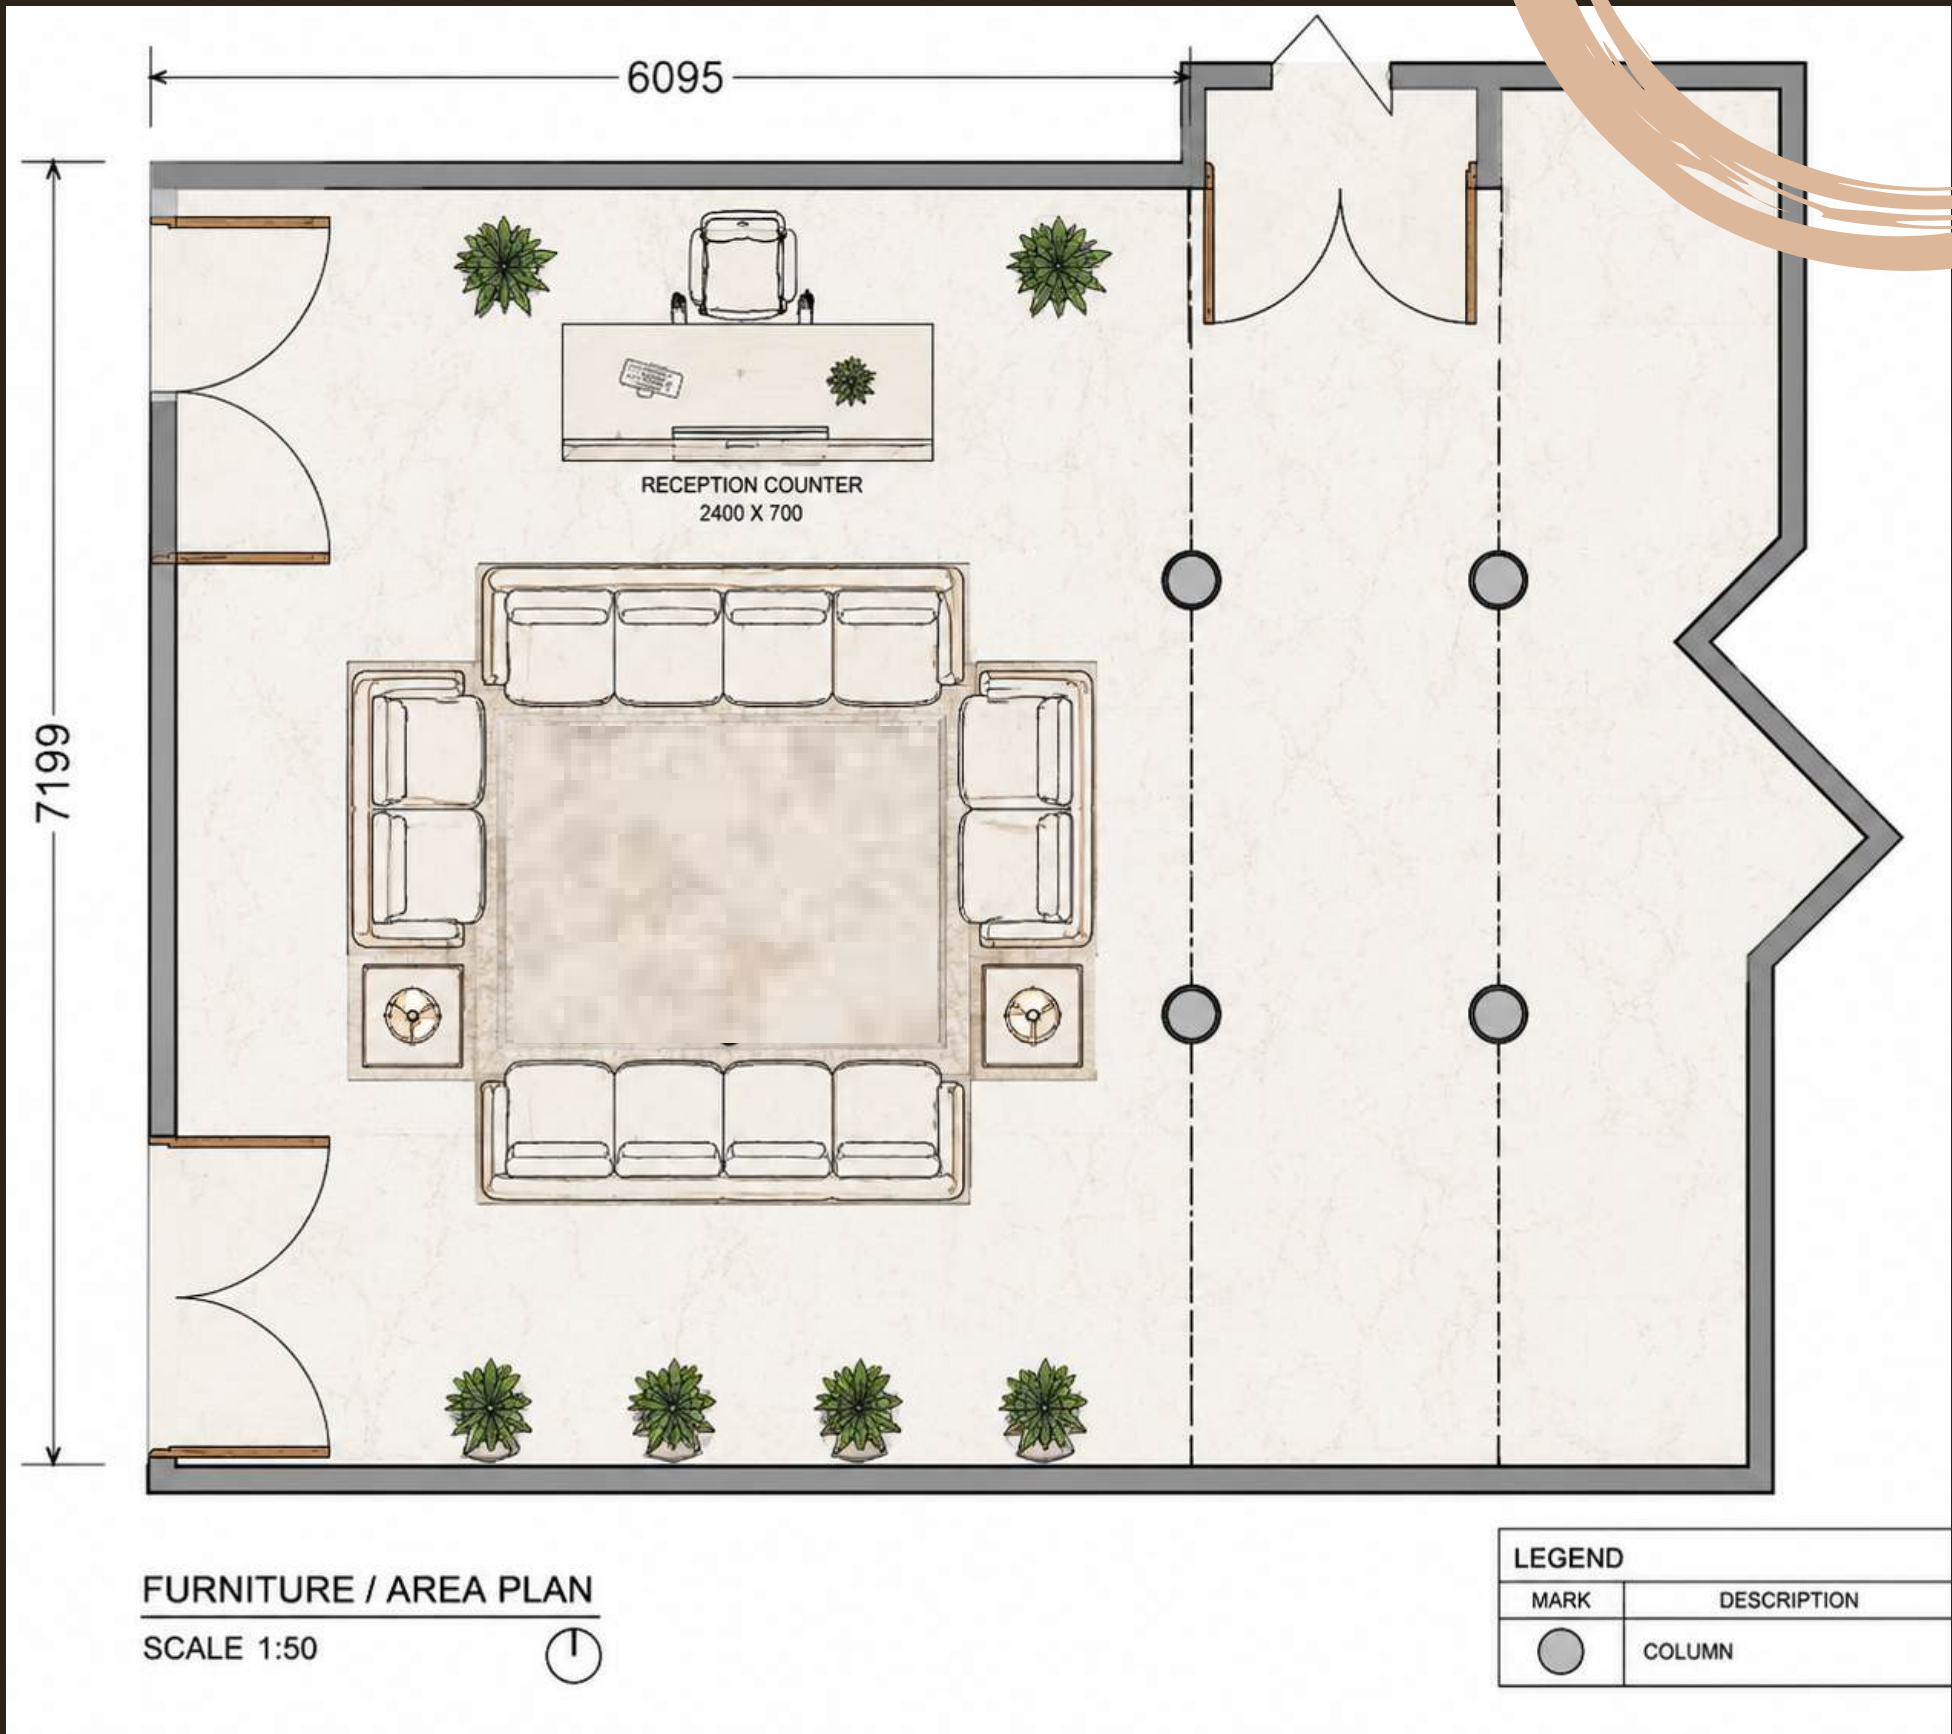



“craftsmanship, and timeless aesthetics of Jammu & Kashmir through a modern design approach”


“Jammu & Kashmir in a modern institutional setting”




Project 04




**PROPOSED RAJKIYA SARVODAYA. KANYA
VIDYALAYA, EAST VINOD NAGAR NEW DELHI**

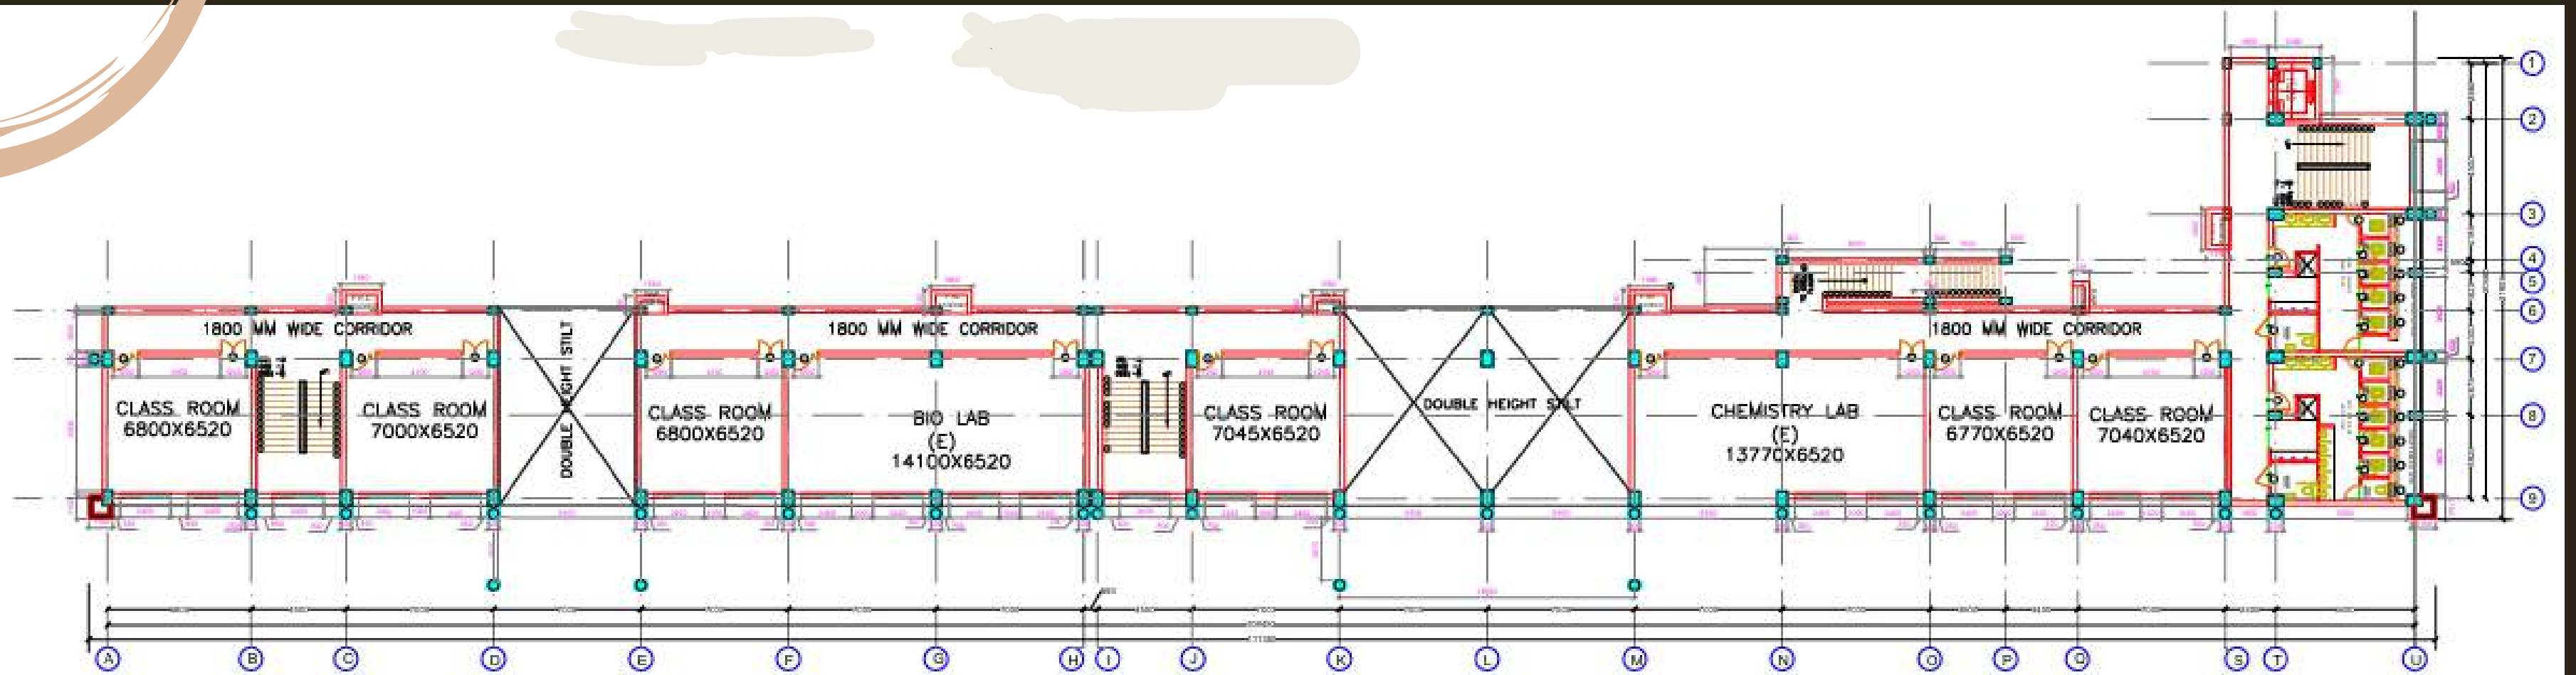


FIRST FLOOR PLAN

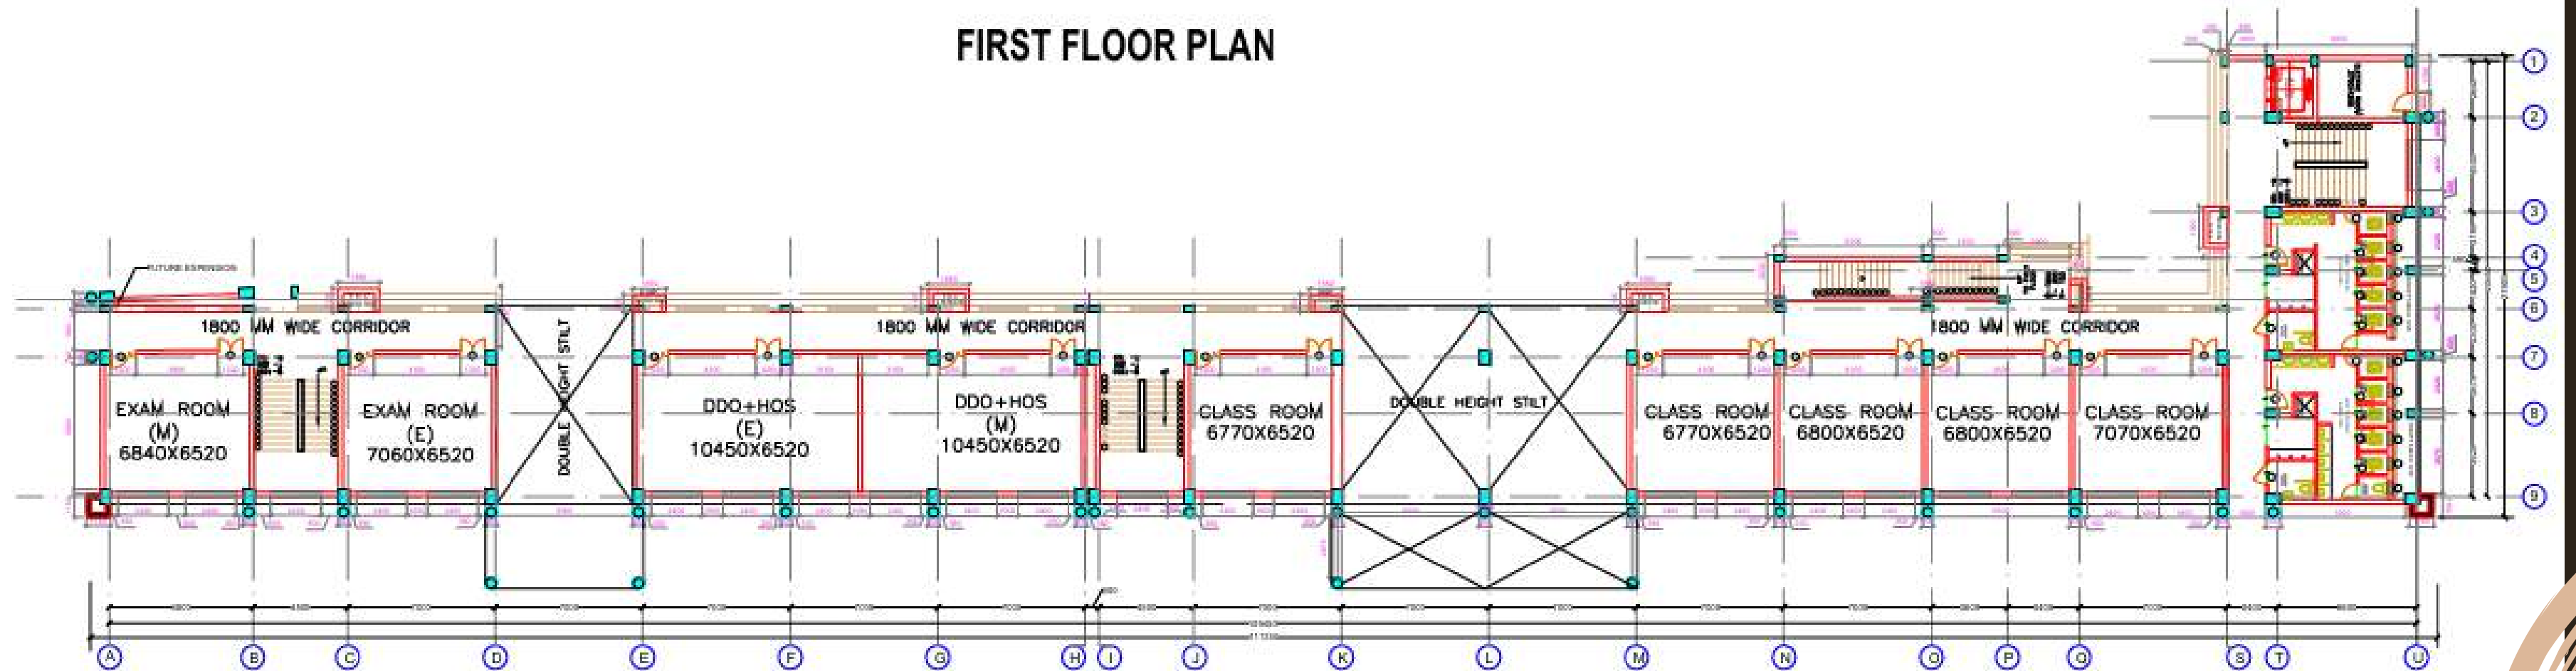


GROUND FLOOR PLAN

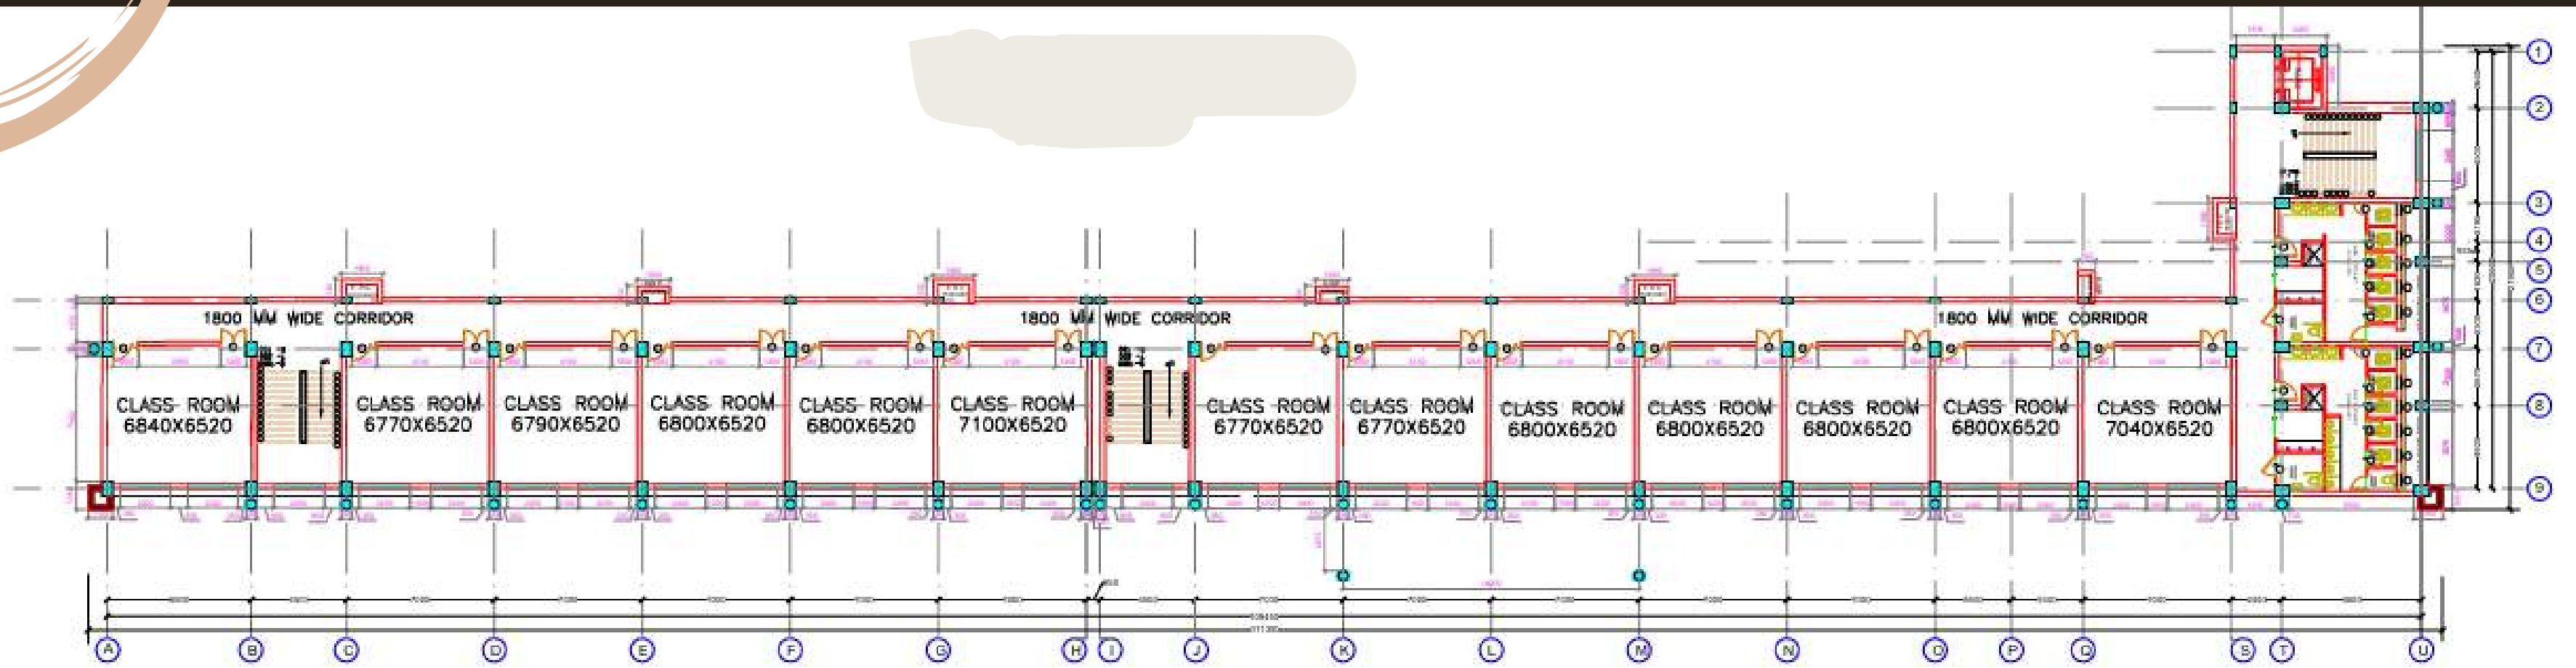


THIRD FLOOR PLAN

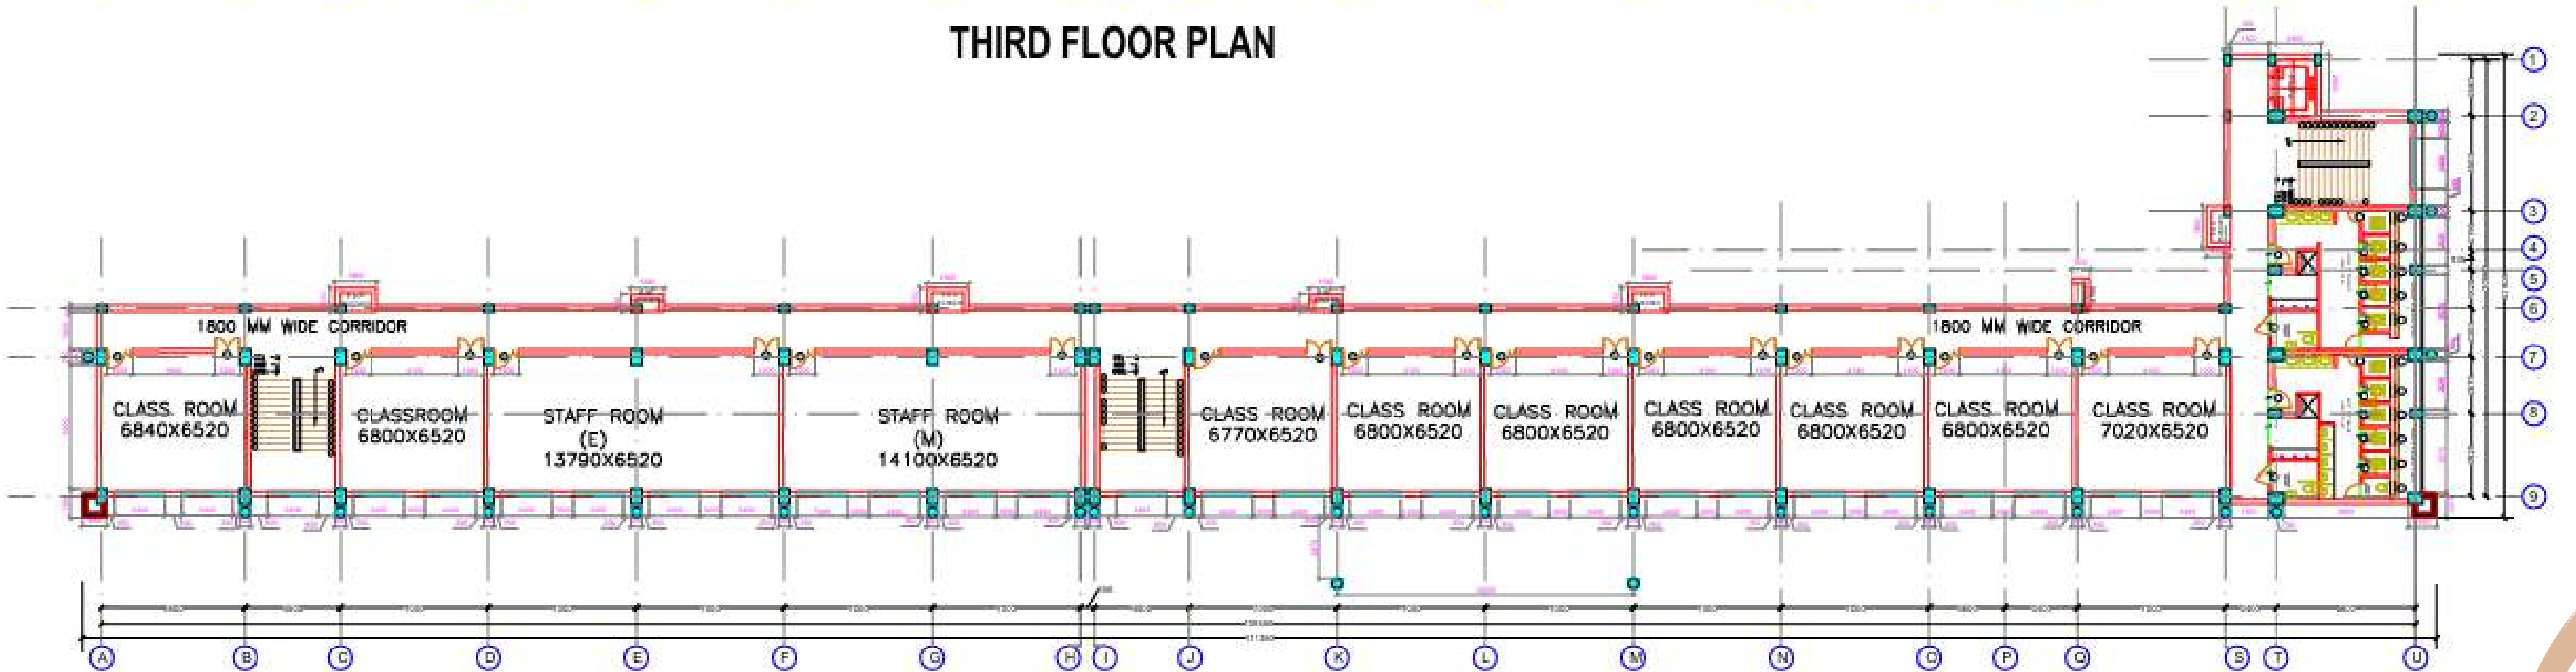


SECOND FLOOR PLAN

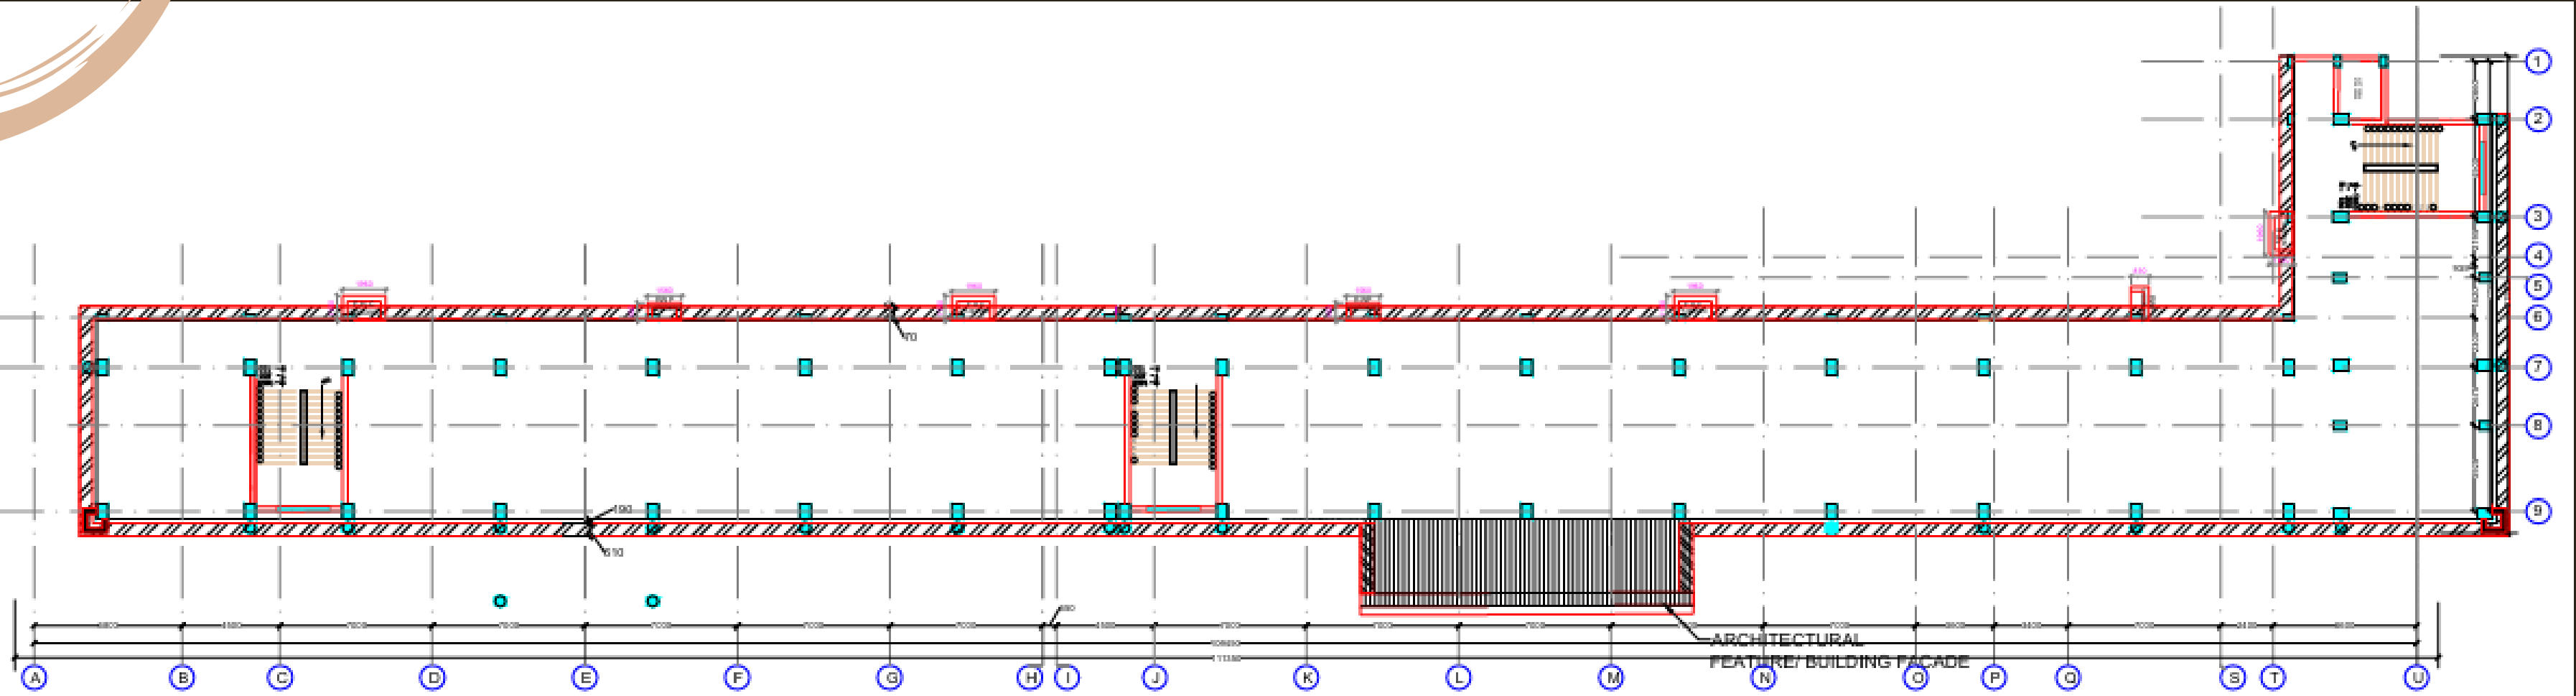

TERRACE FLOOR PLAN

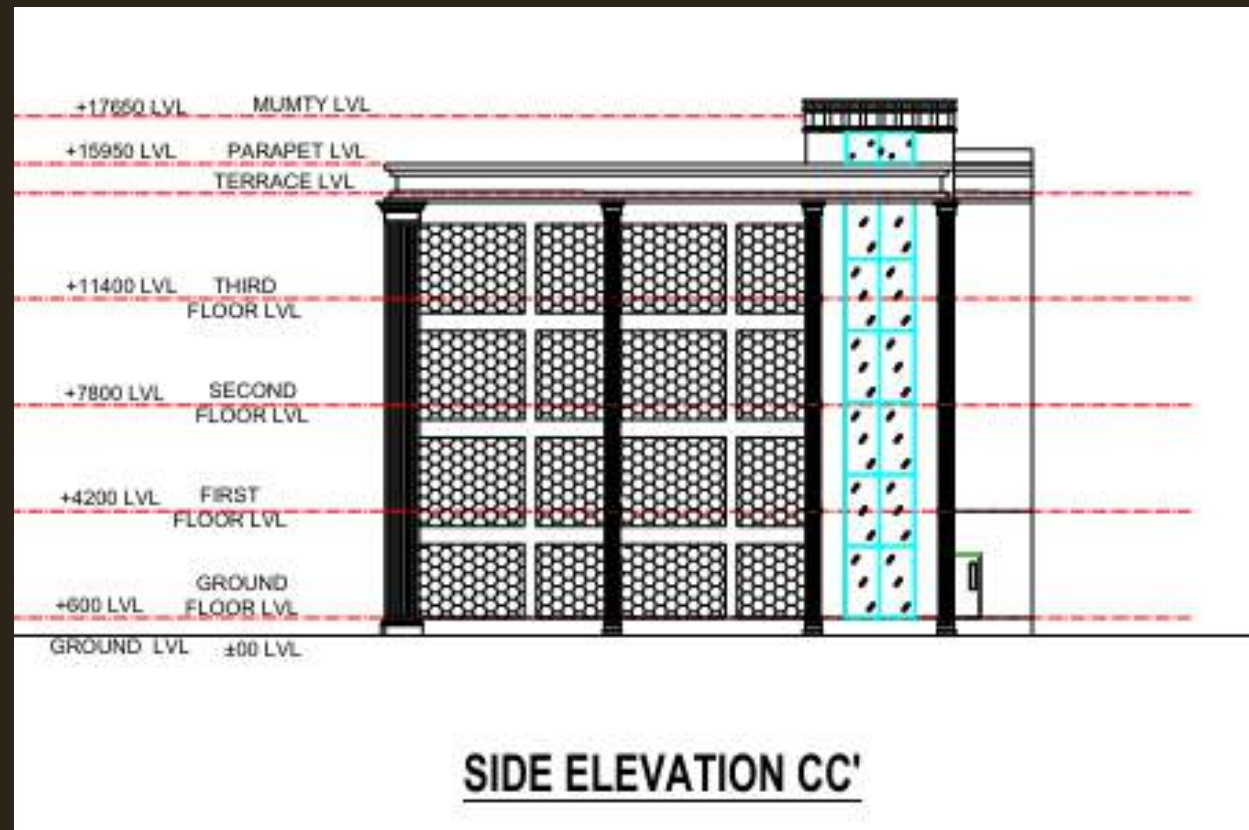


SIDE ELEVATION CC'

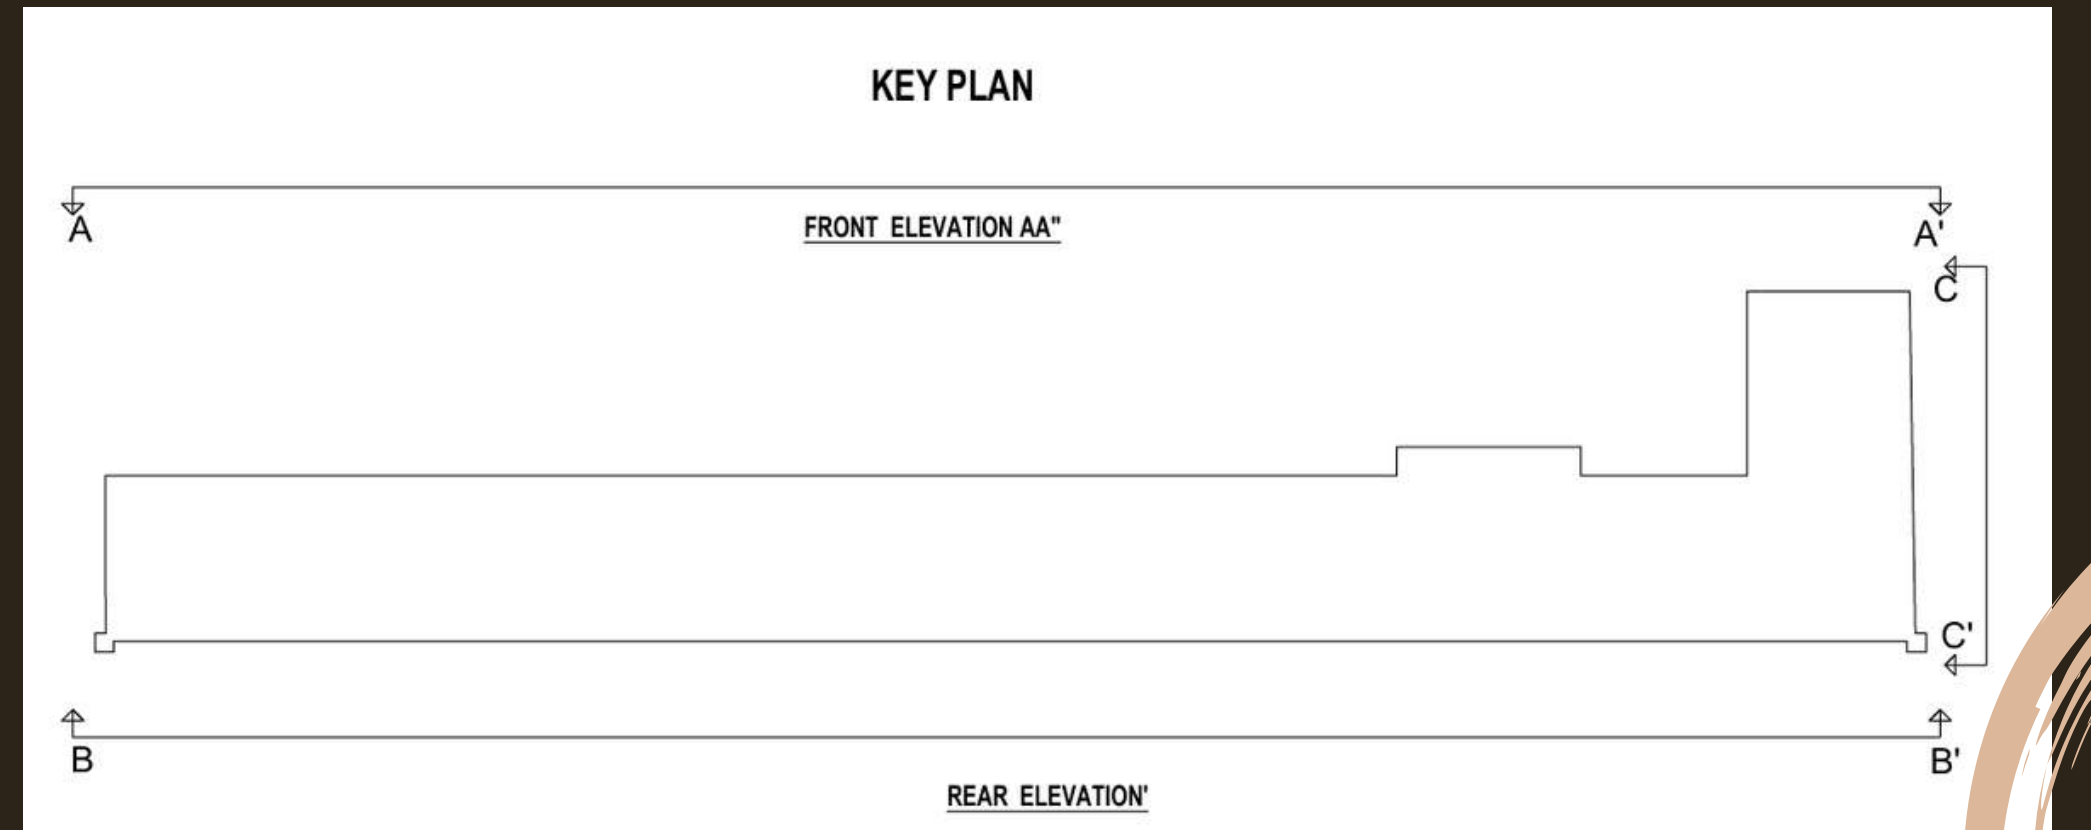

KEY PLAN


FRONT ELEVATION AA"

REAR ELEVATION'

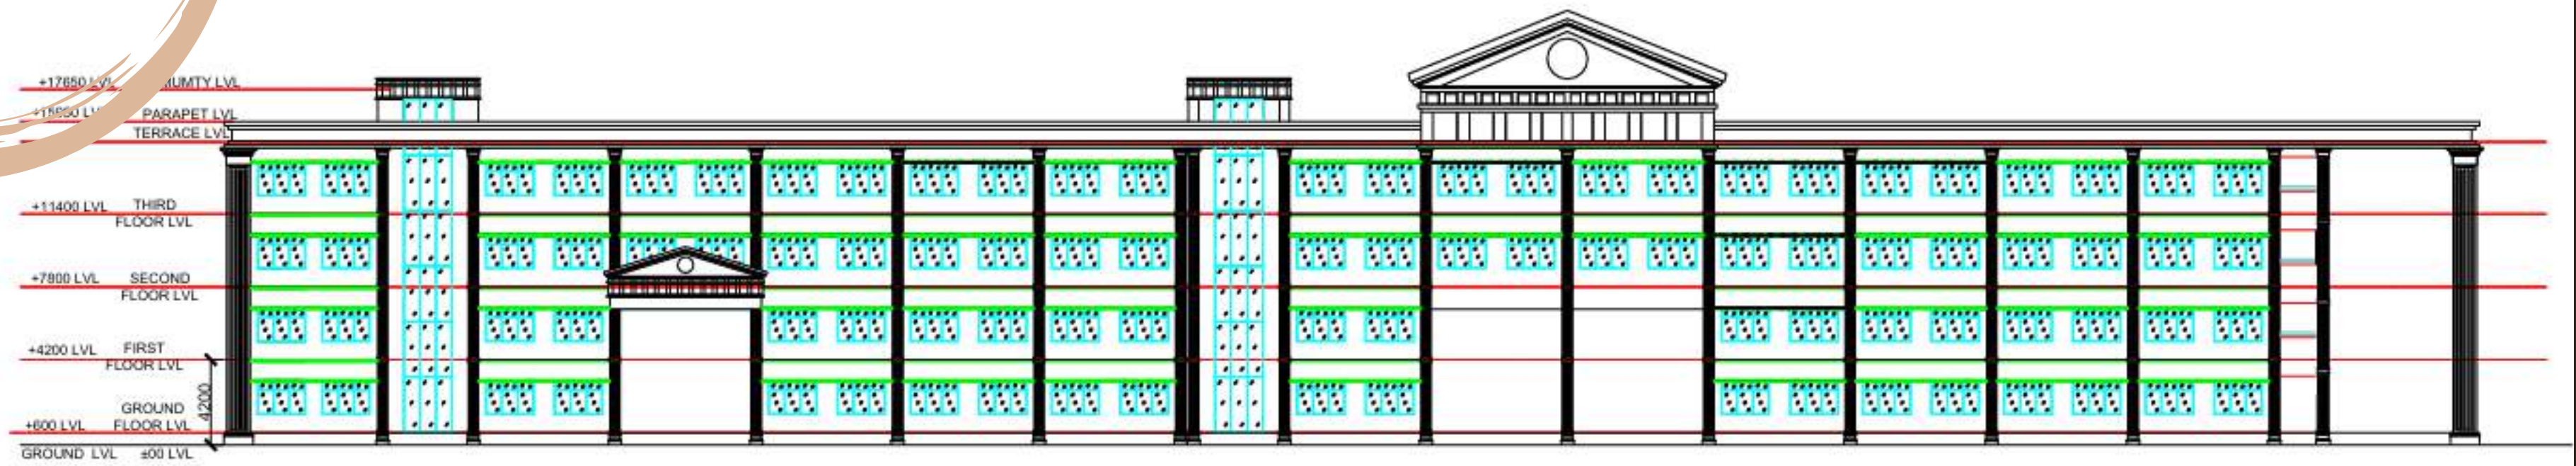


REAR ELEVATION BB'



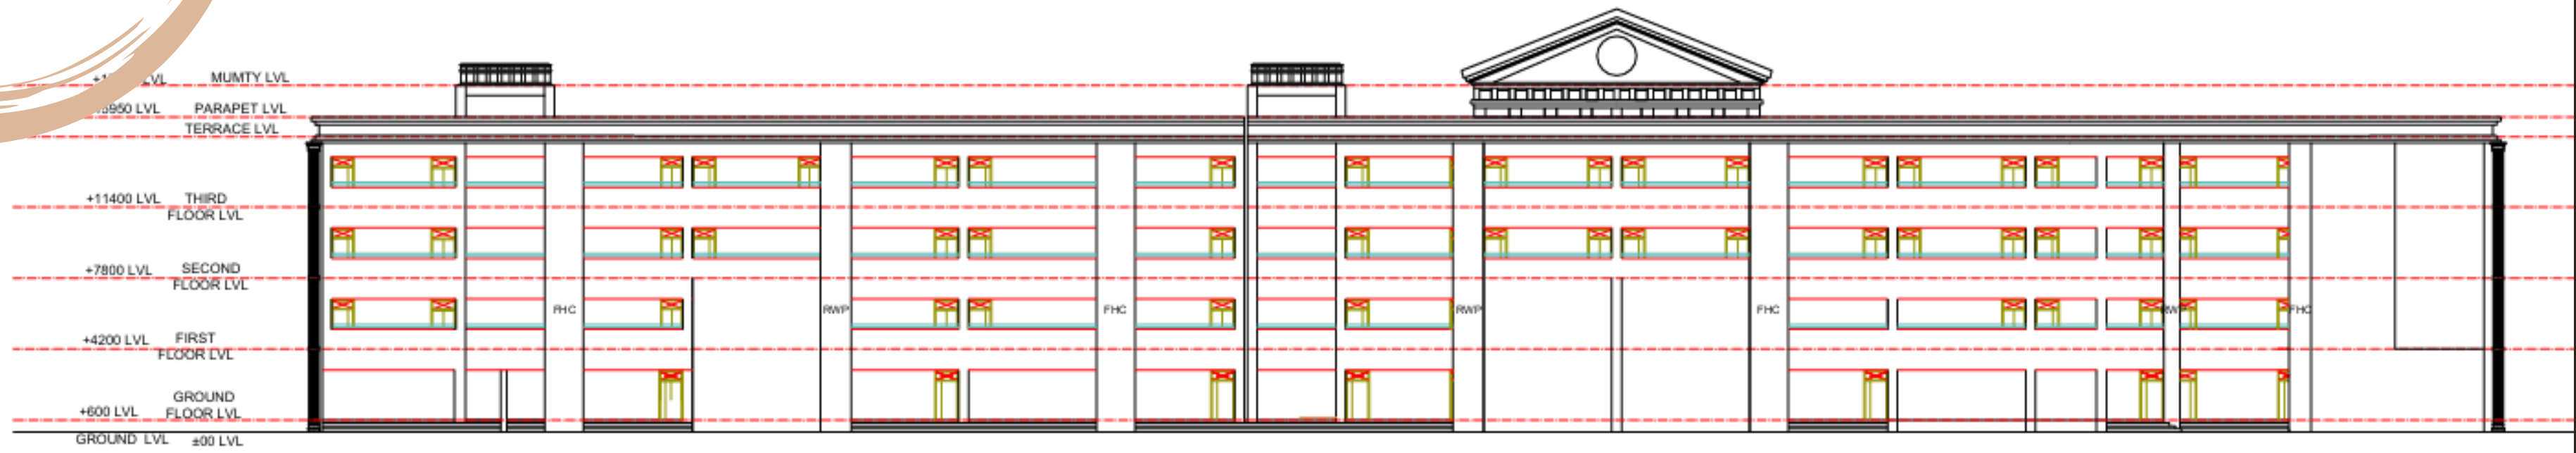

FRONT ELEVATION AA'




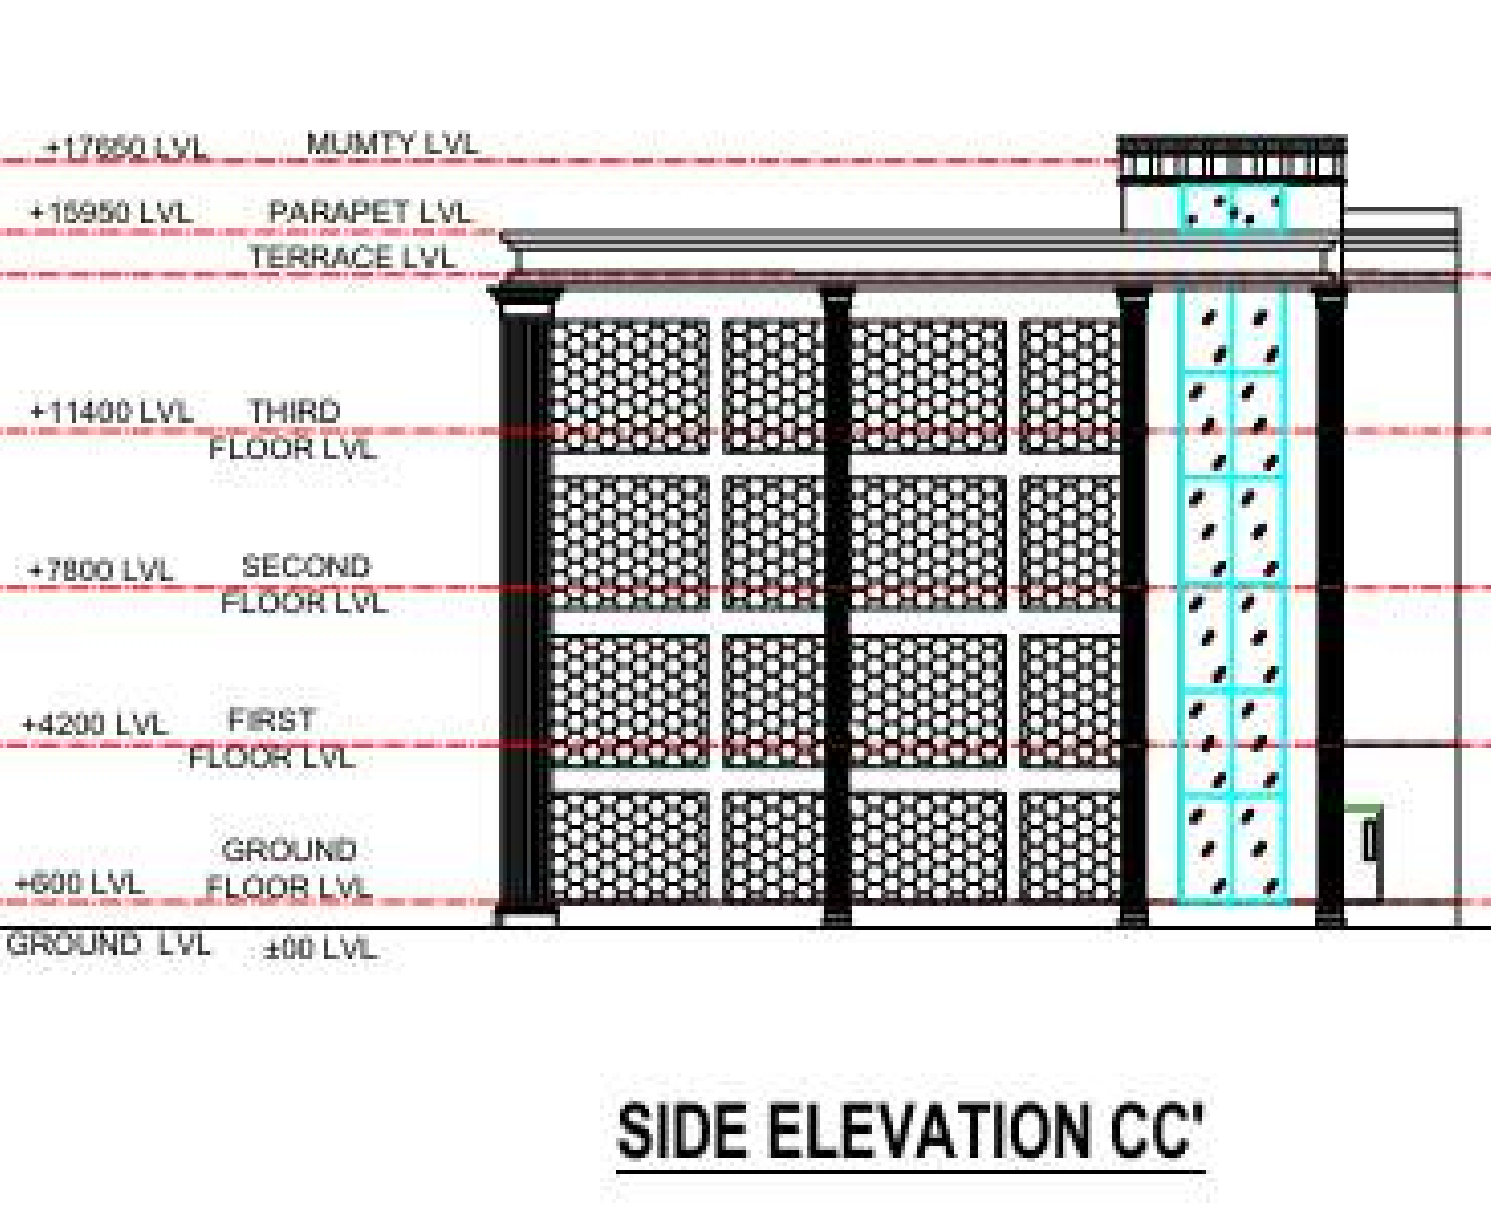


Project 05

DORMATORY, BHATGAON, LUCKNOW




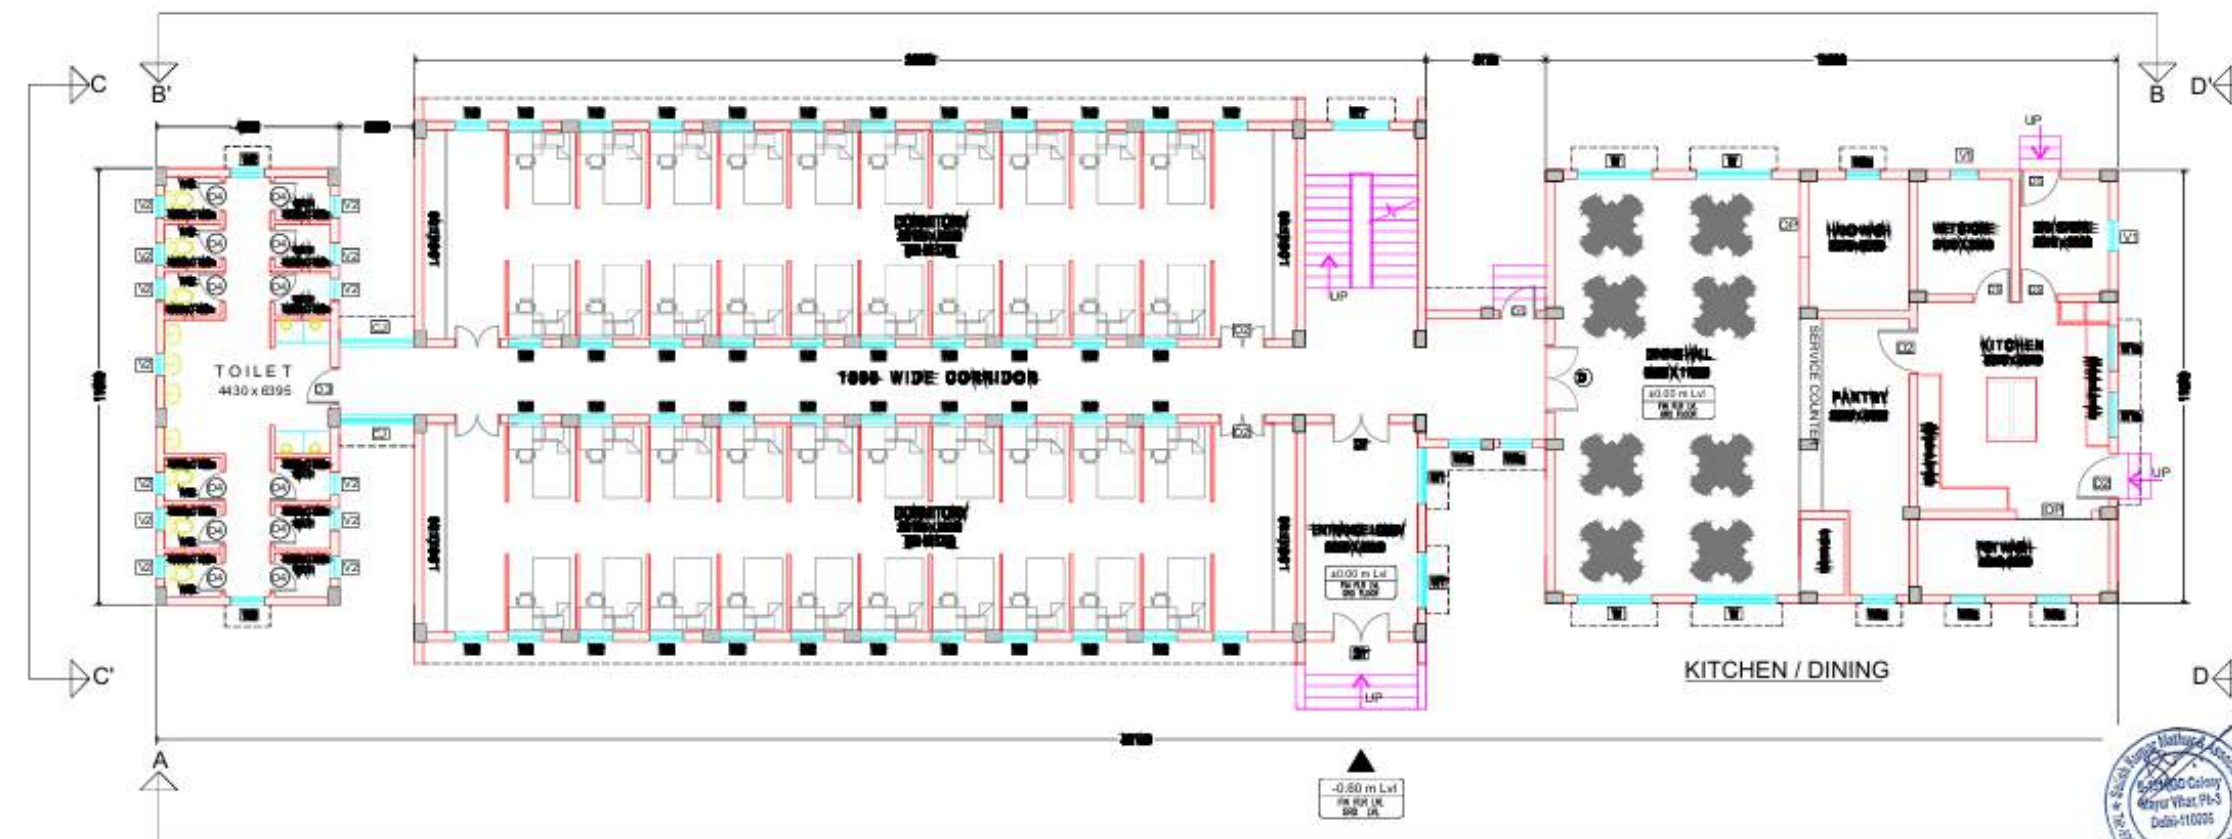

GROUND FLOOR PLAN 620.00 SQMTS

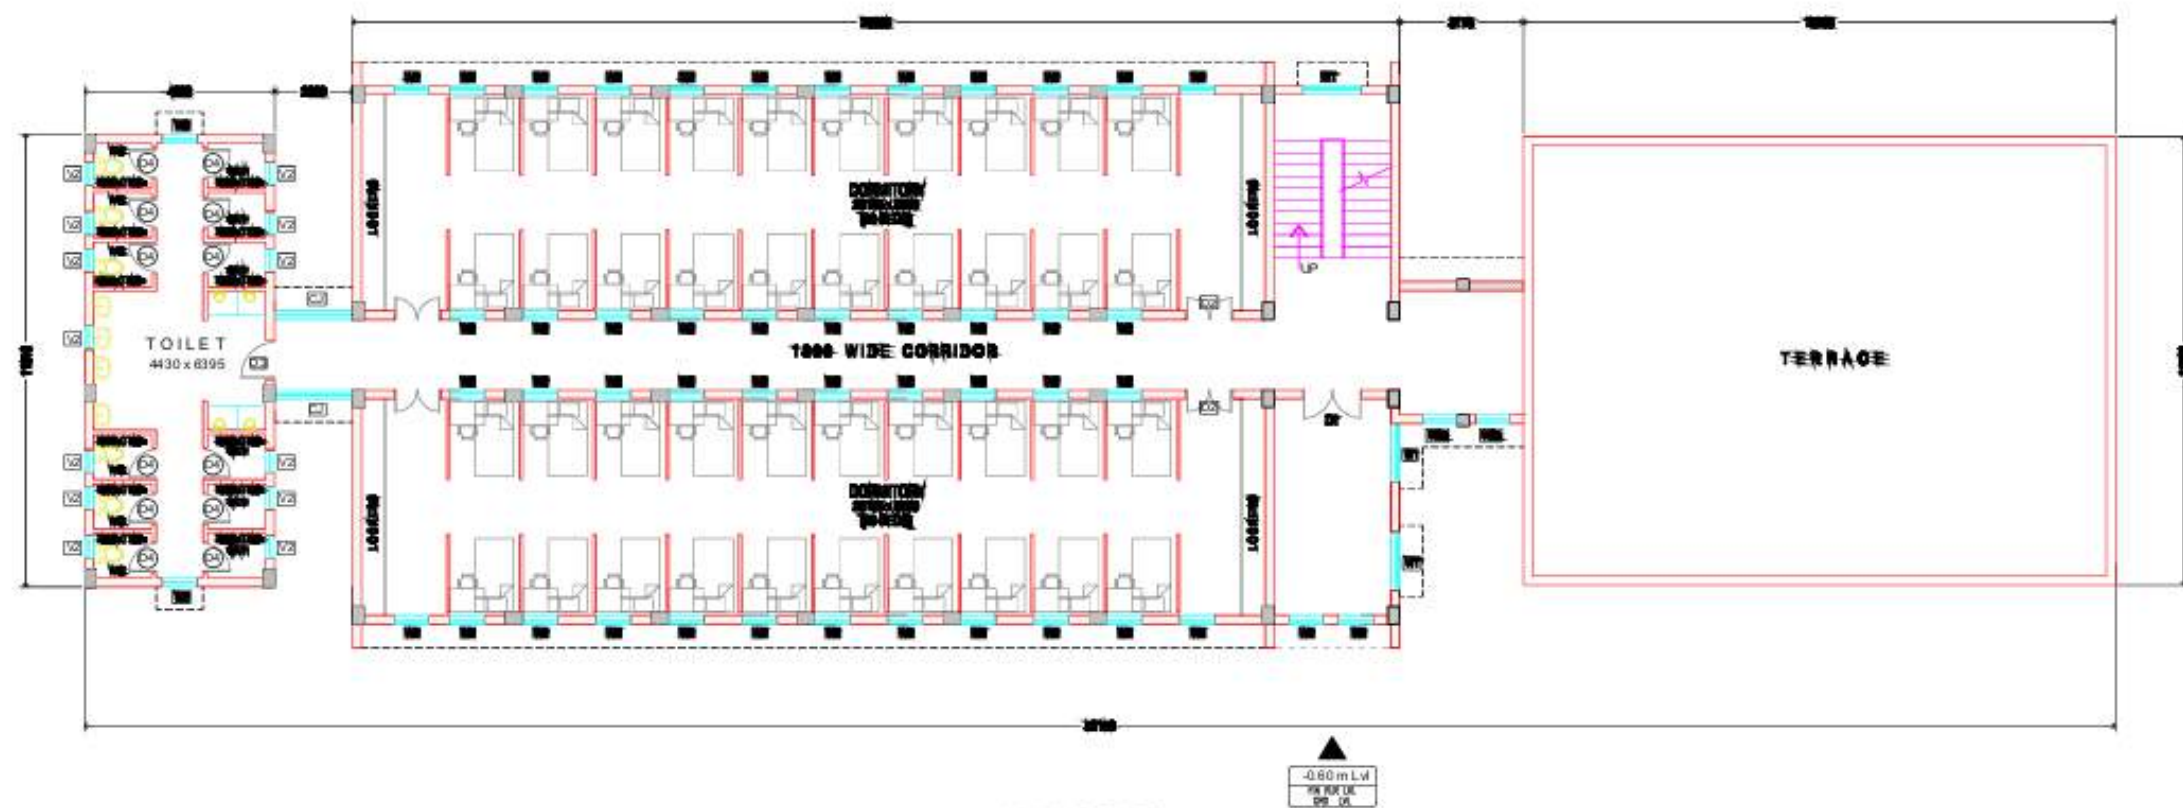


FIRST FLOOR PLAN 445.00 SQMTS

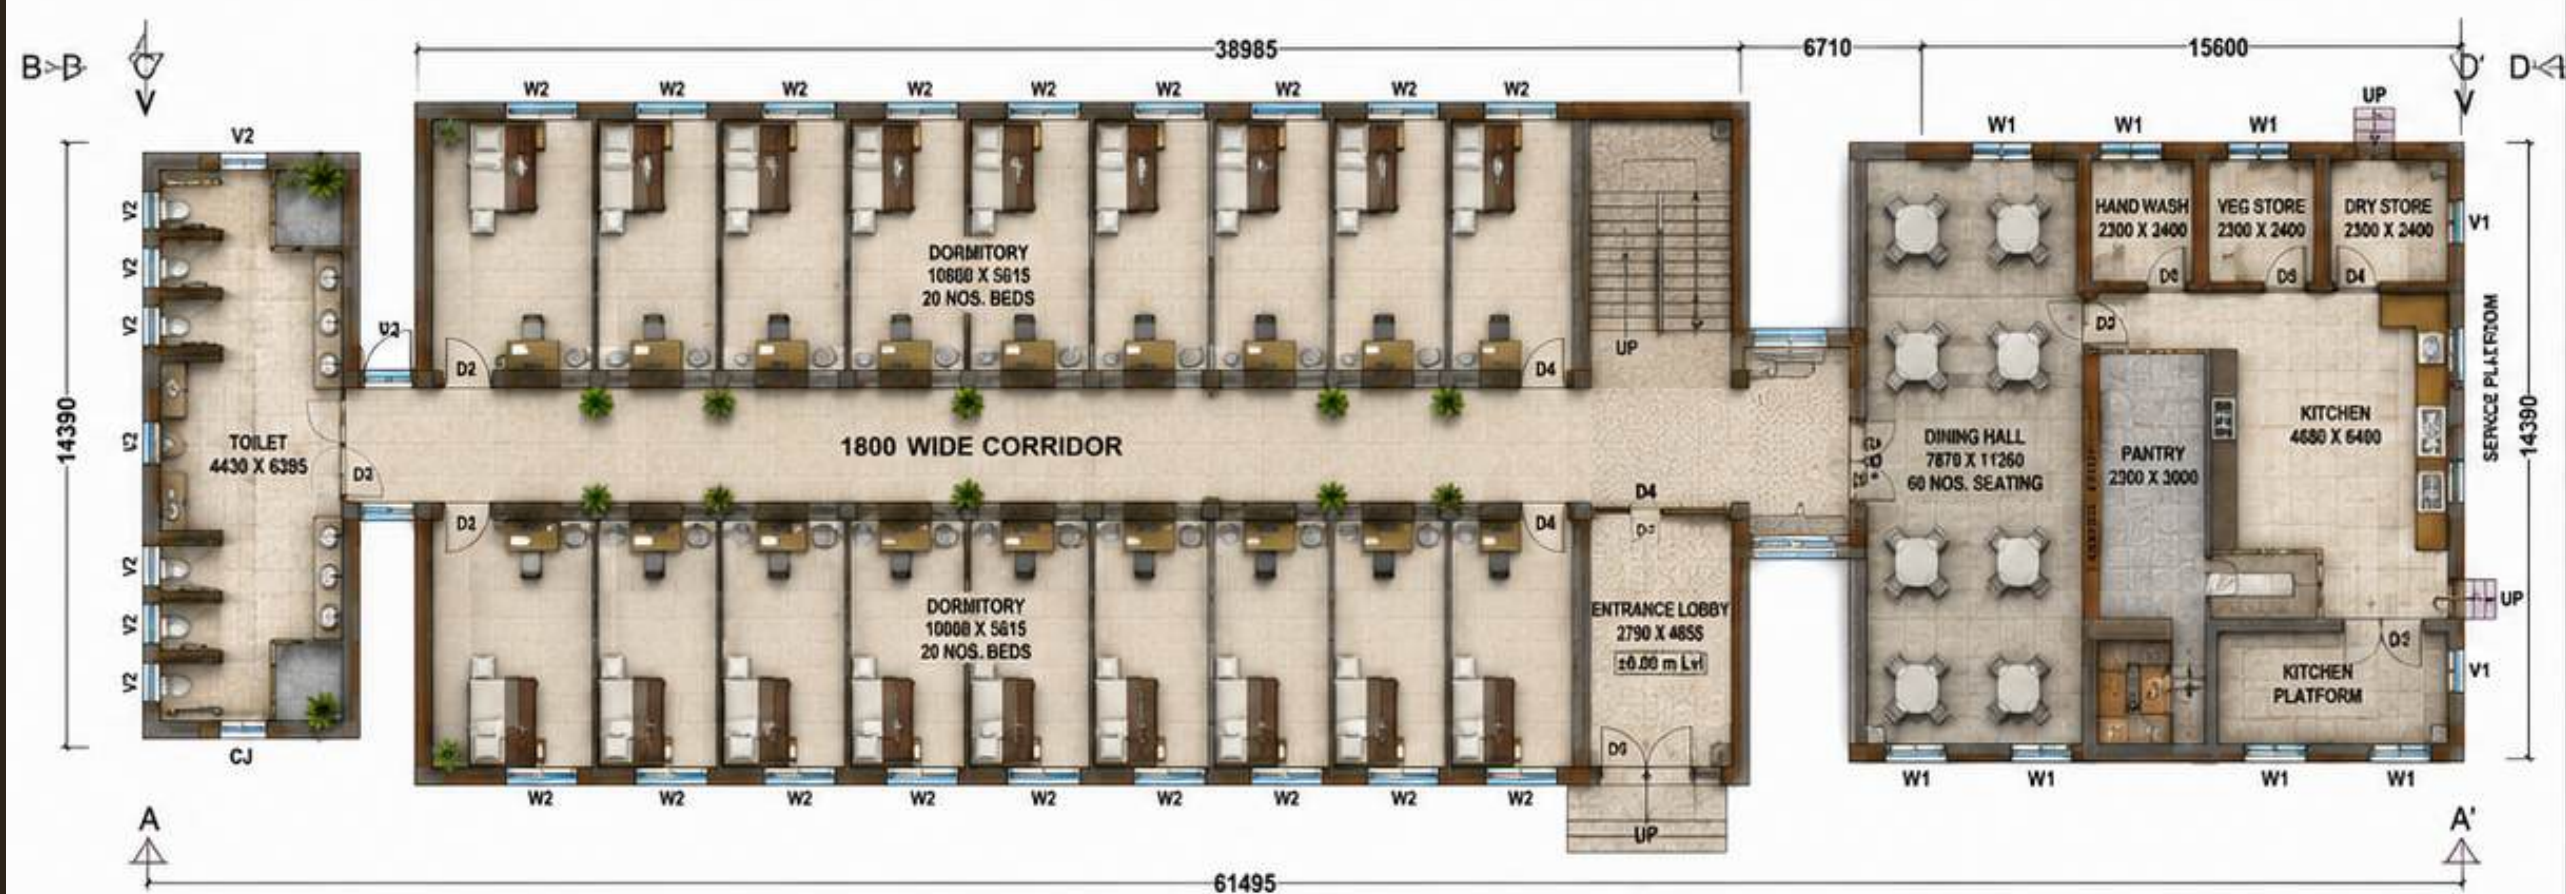





ELEVATION A-A'

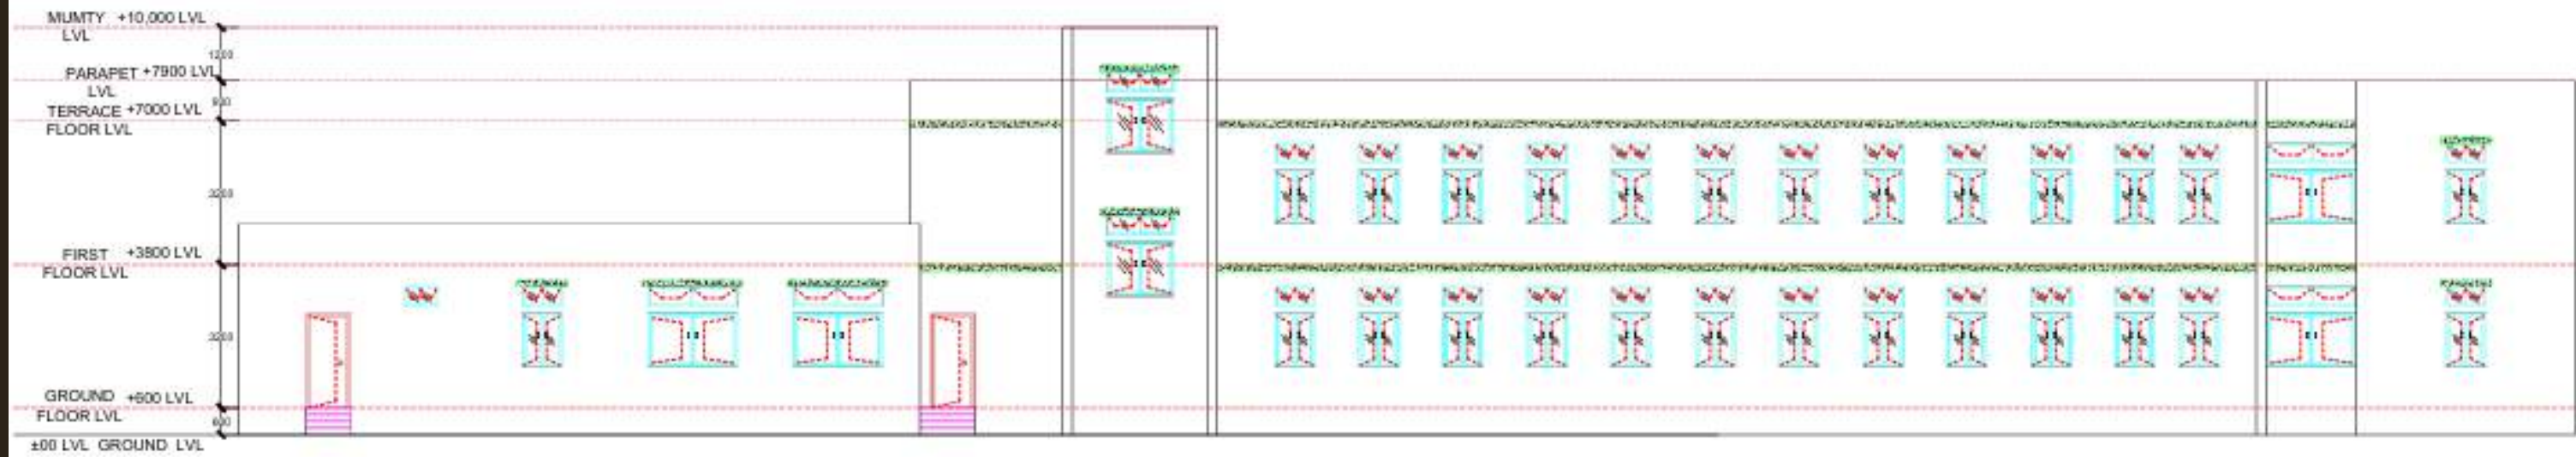

ELEVATION B-B'

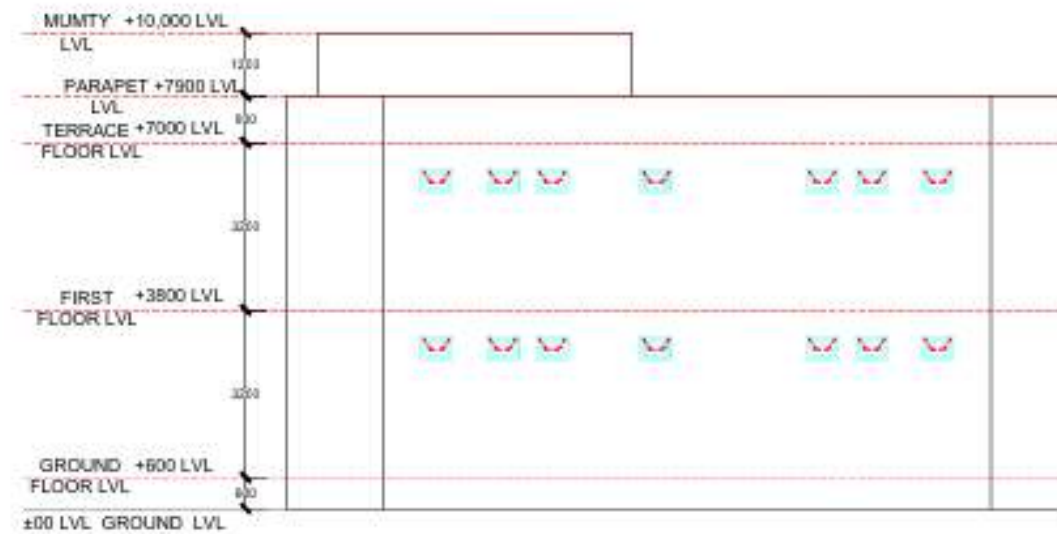

ELEVATION C-C'

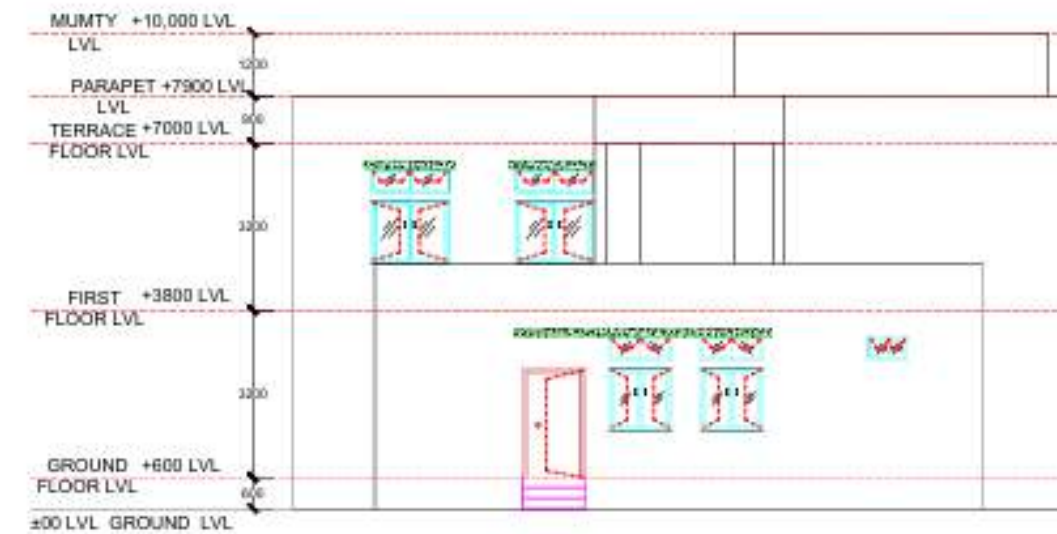

ELEVATION D-D'

MUMTY LVL
+10,000 LVL

PARAPET LVL
+7900 LVL

TERRACE
FLOOR LVL
+7000 LVL

FIRST
FLOOR LVL
+3800 LVL

GROUND
FLOOR LVL
+600 LVL

±00 LVL
GROUND LVL



ELEVATION A-A'

MUMTY LVL
+10,000 LVL

PARAPET LVL
+7900 LVL

TERRACE
FLOOR LVL
+7000 LVL

FIRST
FLOOR LVL
+3800 LVL

GROUND
FLOOR LVL
+600 LVL

±00 LVL
GROUND LVL



ELEVATION B-B'

MUMTY LVL
+10,000 LVL


PARAPET LVL
+7900 LVL

TERRACE
FLOOR LVL
+7000 LVL

FIRST
FLOOR LVL
+3800 LVL

GROUND
FLOOR LVL
+600 LVL

±00 LVL
GROUND LVL

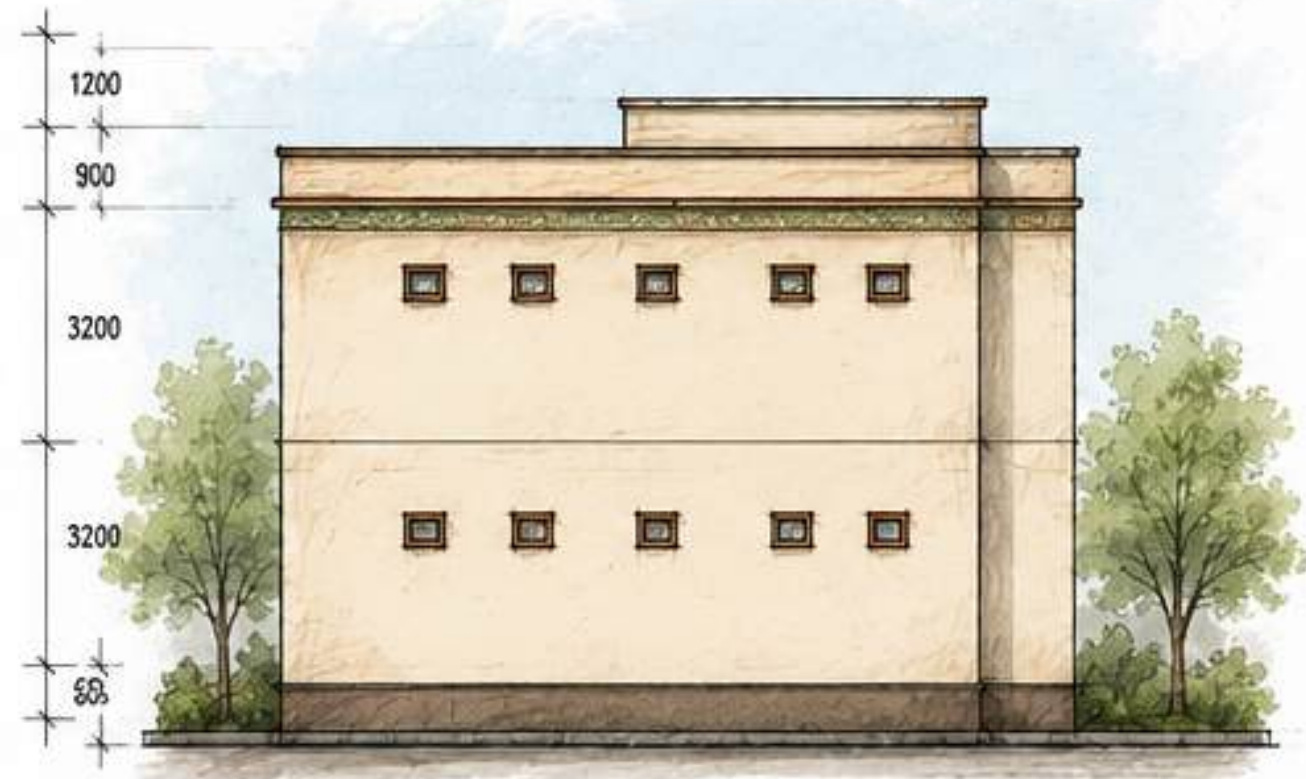

ELEVATION C

MUMTY LVL
+10,000 LVL

PARAPET LVL
+7900 LVL

TERRACE
FLOOR LVL
+7000 LVL

FIRST
FLOOR LVL
+3800 LVL

GROUND
FLOOR LVL
+600 LVL

±00 LVL
GROUND LVL





ELEVATION D-D'

Project 06


MISCELLANEOUS DRAWINGS



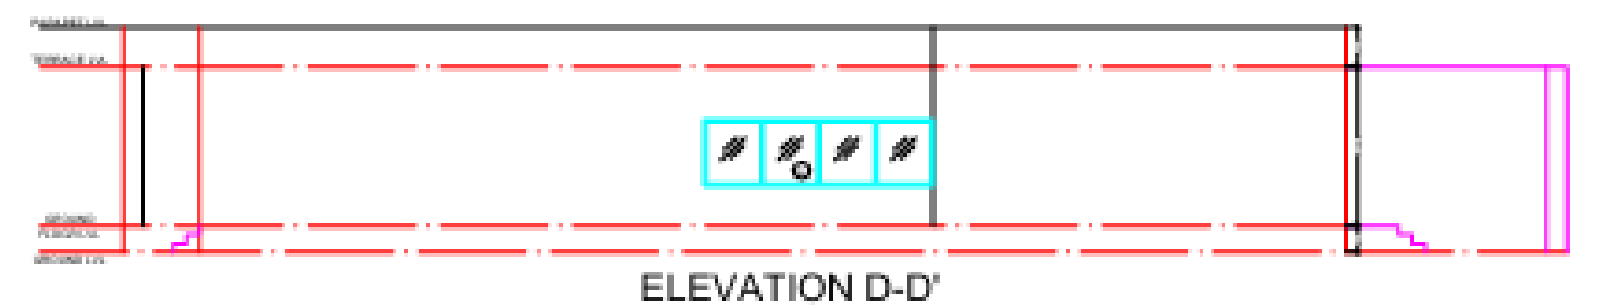


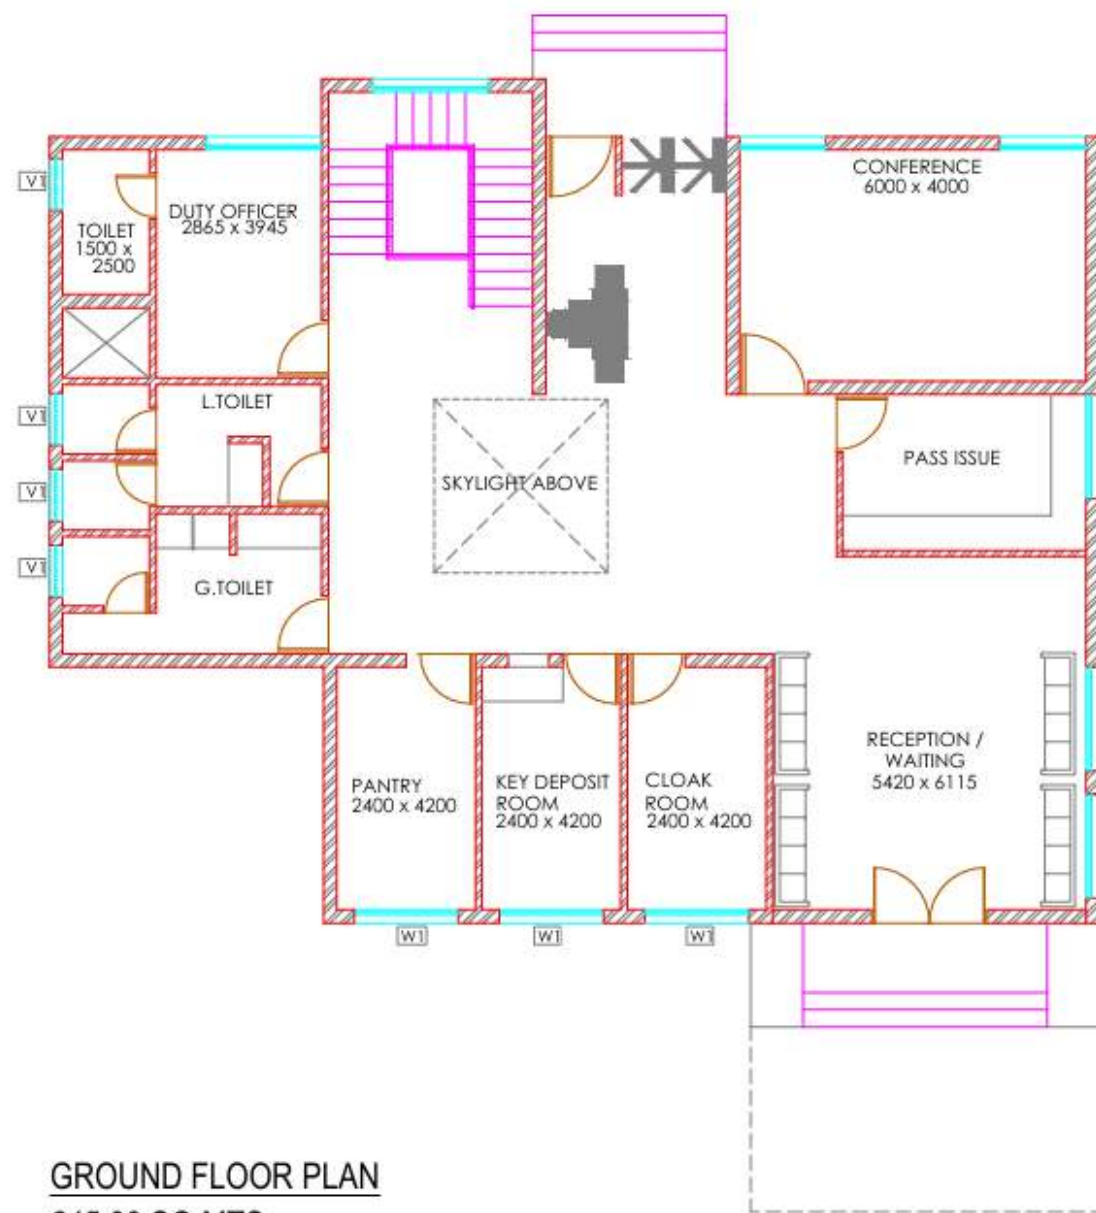

GROUND FLOOR PLAN
245.00 SQ.MTS

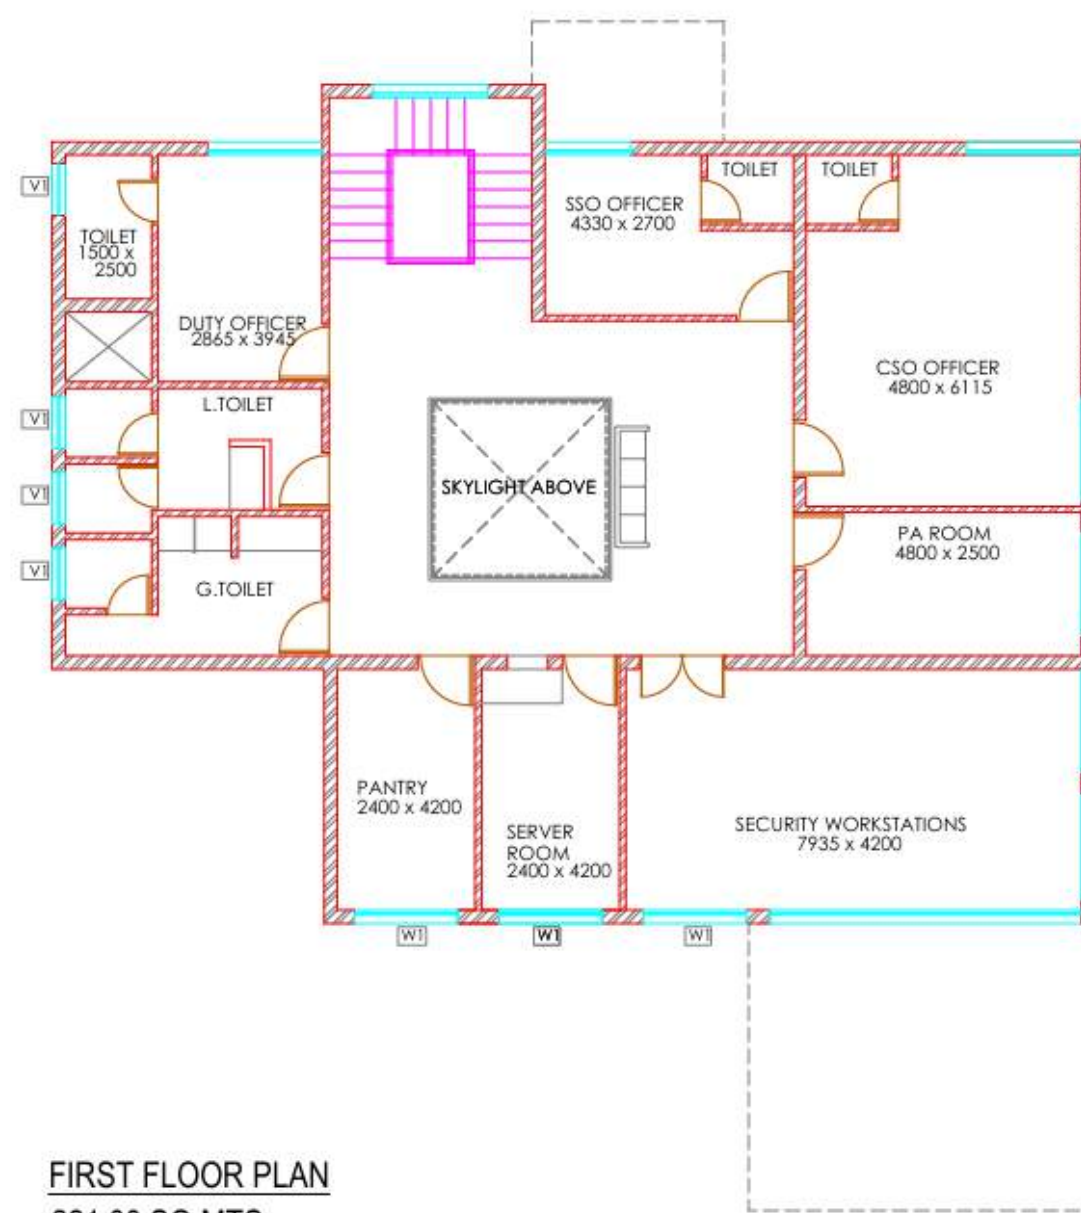

FIRST FLOOR PLAN
221.00 SQ.MTS

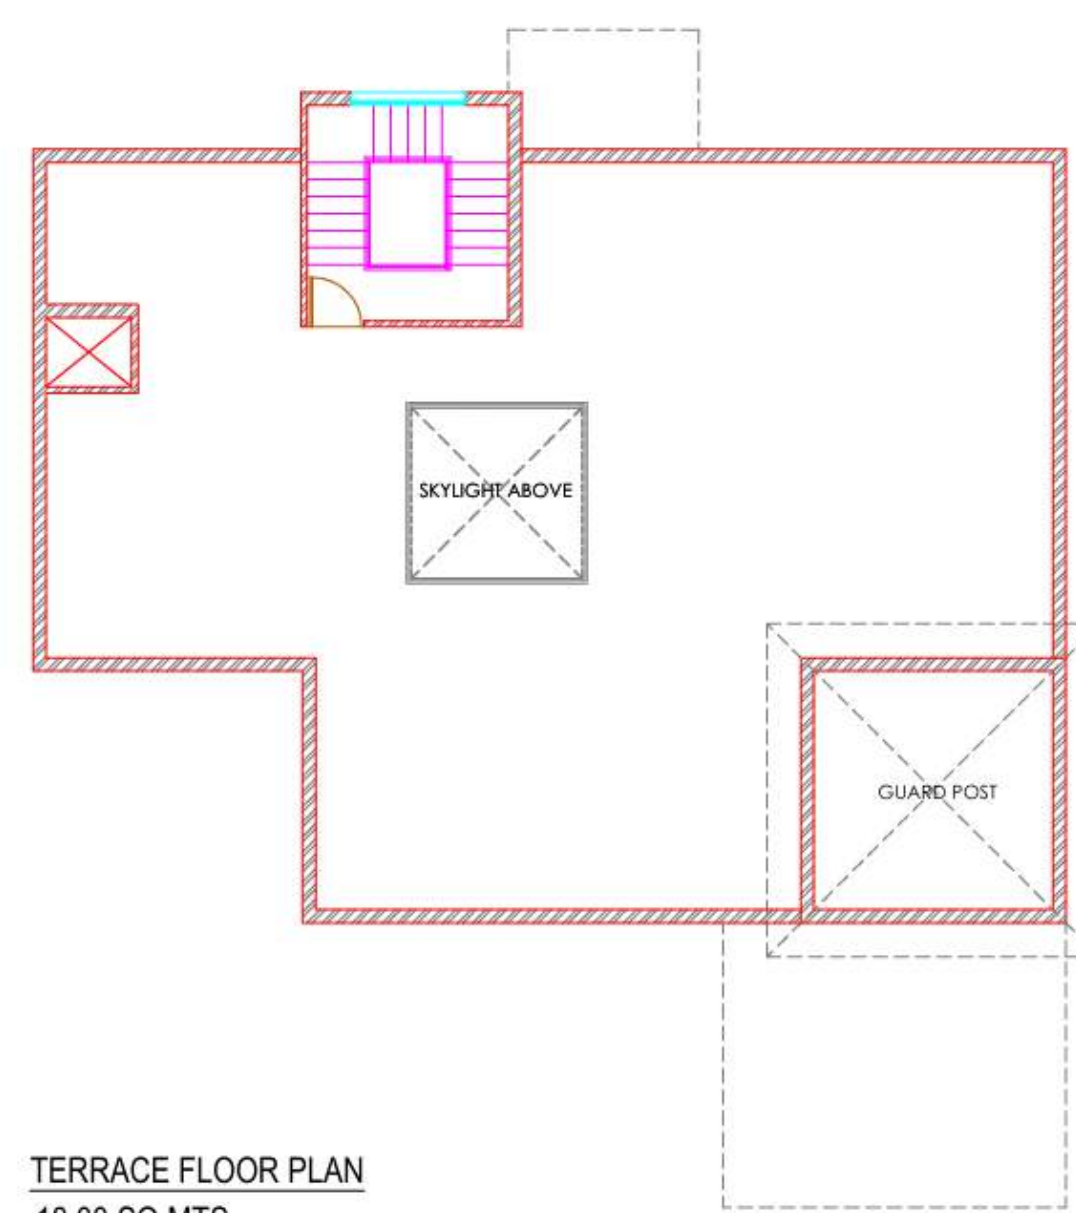

TERRACE FLOOR PLAN
18.00 SQ.MTS



OFFICE INTERIOR



PATHWAY LANDSCAPE

Thank You



+971-522911906



sheikhsameer.prof@gmail.com



**Burjuman, Dubai, United Arab
Emirates**

